


LESTE / OESTE HIPOTÉTICOS — CONFIRMAR SOL

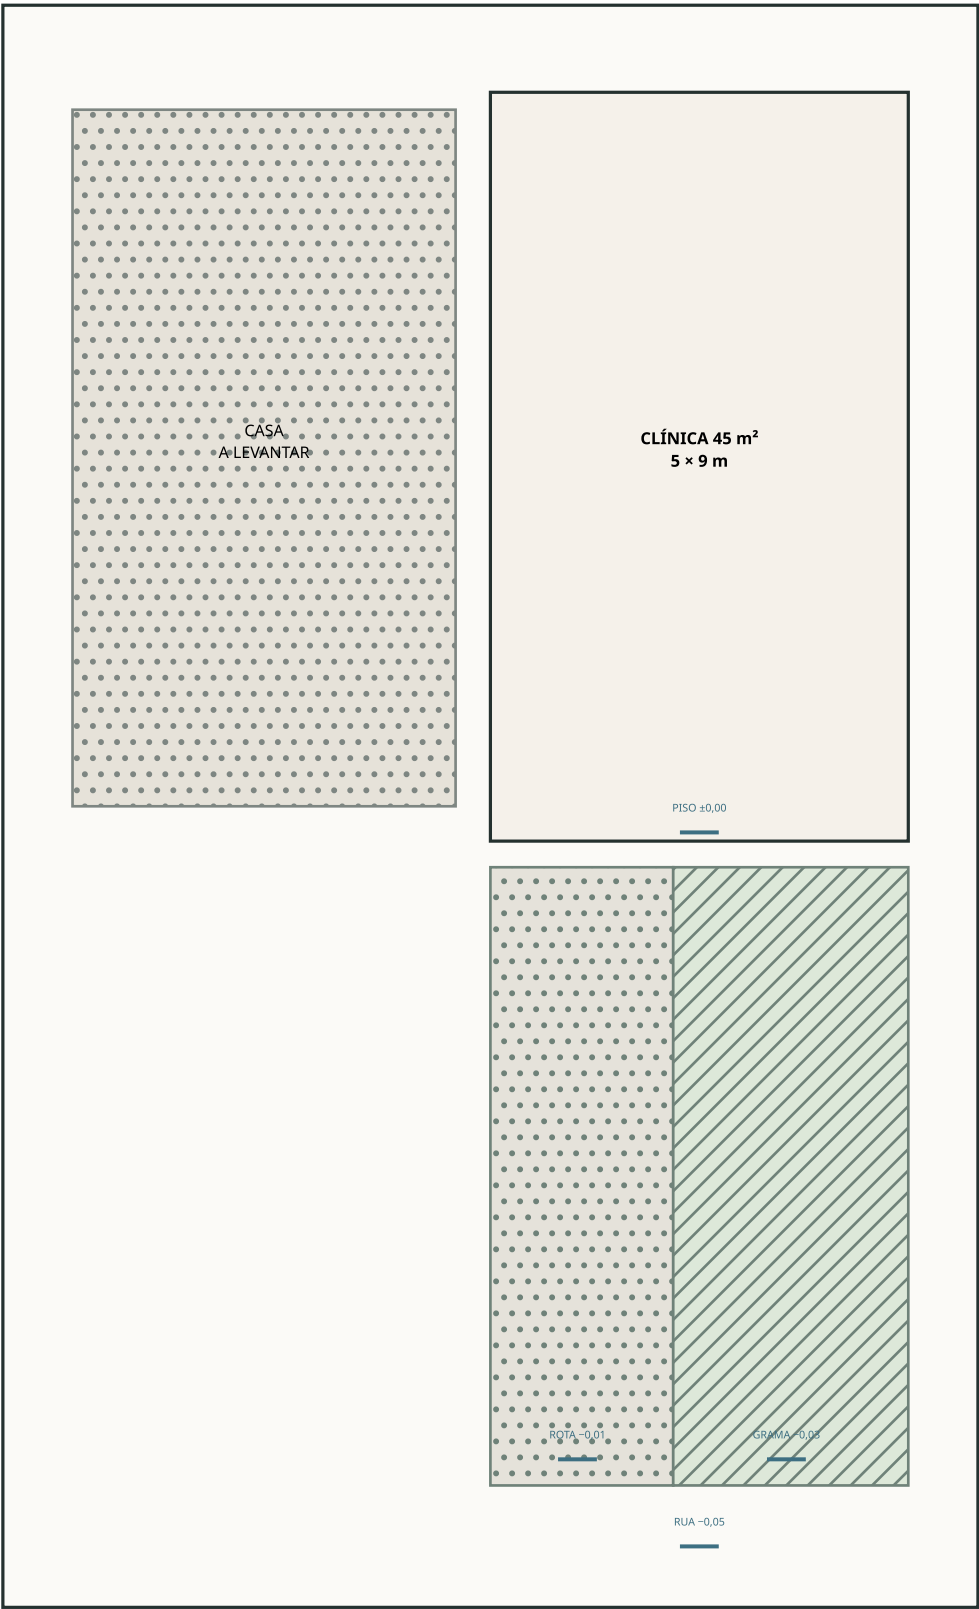

LUMINA

SKIN INTELLIGENCE

C-I01

IMPLANTAÇÃO BASE

Hipótese de lote 12 × 20 m; substituir pelo levantamento


ALTERNATIVA COMPACTA

Envoltória	5,00 × 9,00 m
Área bruta	45,00 m²
Operação	1 atendimento
Circulação	1,20 m
Implantação	Maior de 2027
Status	Comparativo

Clínica Lumina Skin Intelligence

Alternativa compacta ajustável

Conferir no local • RRT/ART obrigatórias

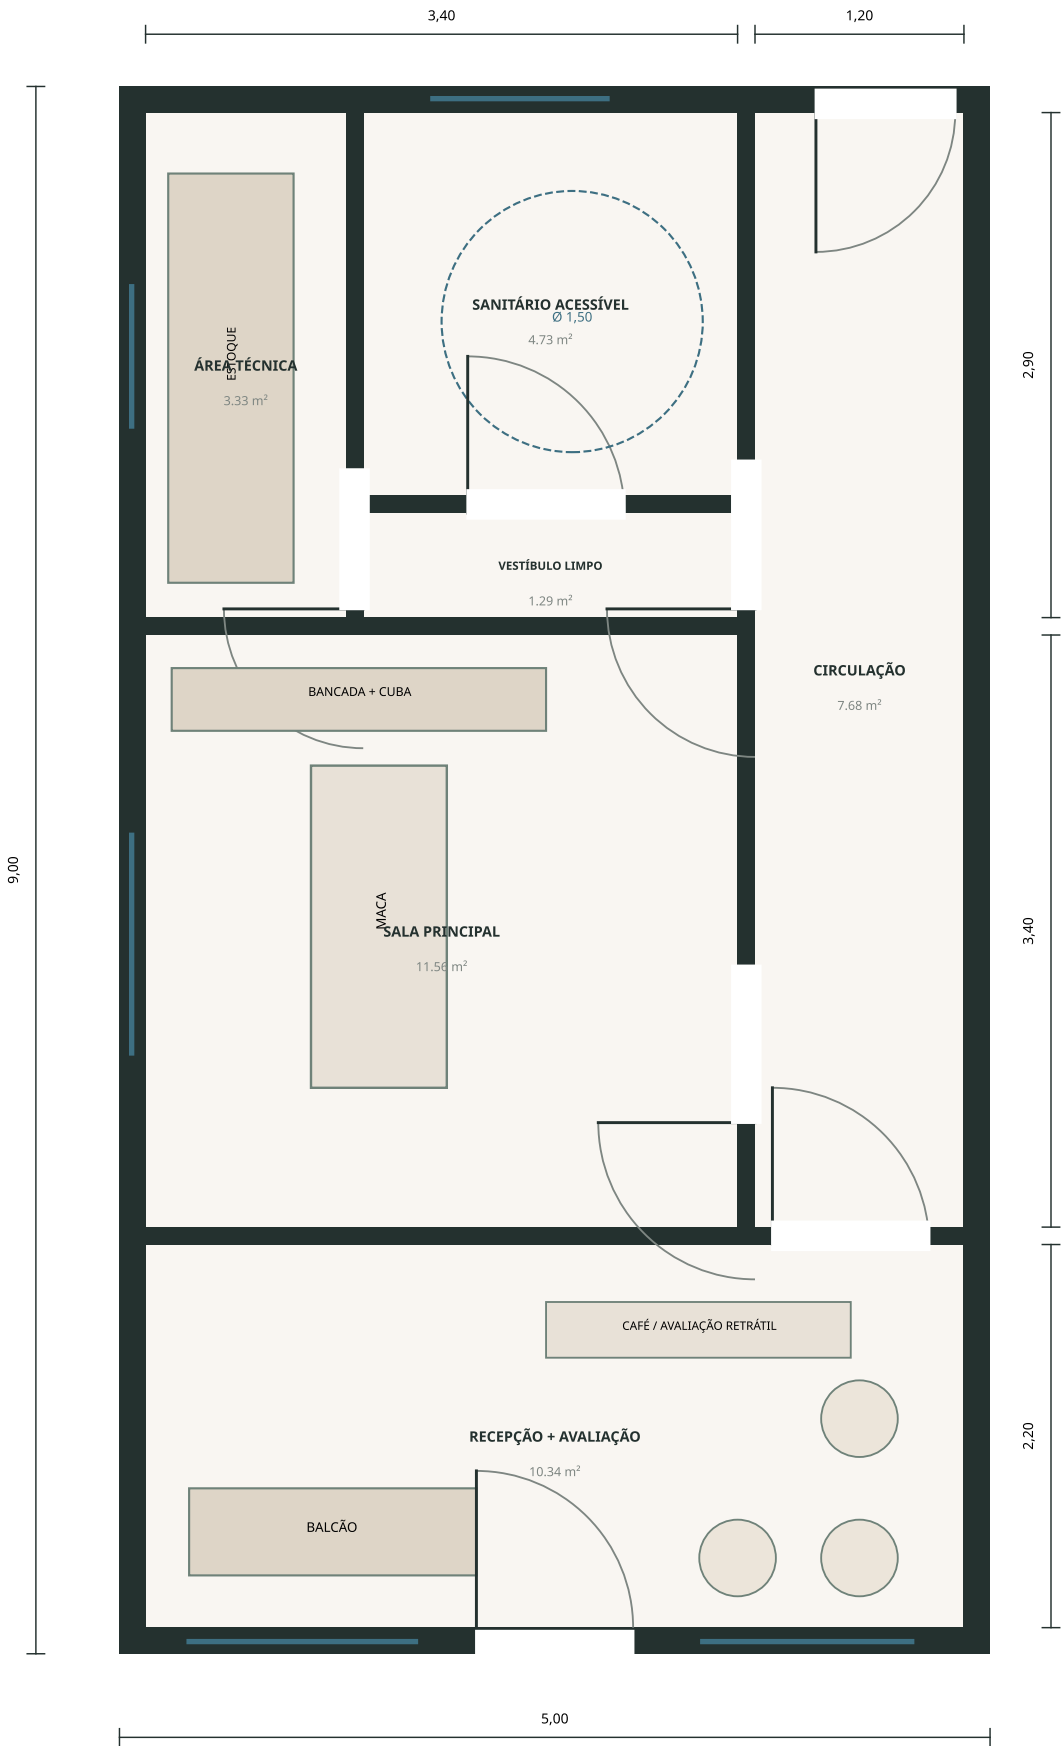

LUMINA

SKIN INTELLIGENCE

C-A01

PLANTA COTADA + LAYOUT

Alternativa compacta — 5,00 × 9,00 m

ALTERNATIVA COMPACTA

Envoltória	5,00 × 9,00 m
Área bruta	45,00 m²
Operação	1 atendimento
Circulação	1,20 m
Implantação	Maior de 2027
Status	Comparativo


QUADRO DE ÁREAS

Recepção + avaliação	10.34 m²
Sala principal	11.56 m²
Circulação	7.68 m²
Área técnica	3.33 m²
Vestíbulo limpo	1.29 m²
Sanitário acessível	4.73 m²

Clínica Lumina Skin Intelligence

Alternativa compacta ajustável

Conferir no local • RRT/ART obrigatórias

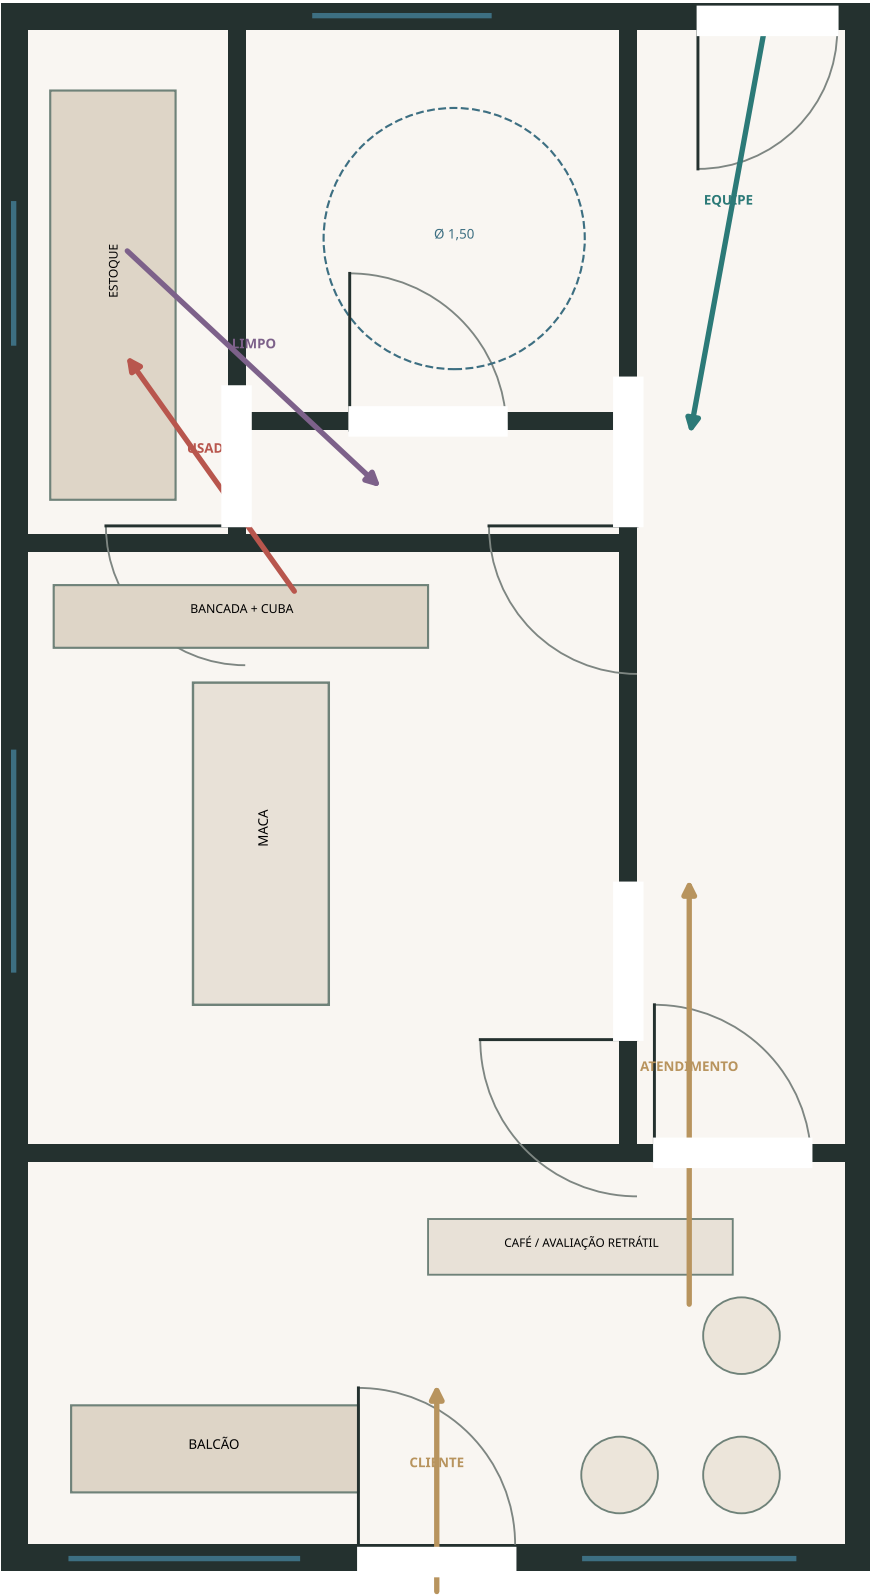

LUMINA

SKIN INTELLIGENCE

C-A02

FLUXOS E SETORIZAÇÃO

Alternativa compacta — 5,00 × 9,00 m

ALTERNATIVA COMPACTA

Envoltória	5,00 × 9,00 m
Área bruta	45,00 m²
Operação	1 atendimento
Circulação	1,20 m
Implantação	Maior de 2027
Status	Comparativo


REGRA

Um atendimento por vez. Materiais limpos e usados seguem recipientes separados. Resíduos saem preferencialmente pelo fundo.

Clínica Lumina Skin Intelligence

Alternativa compacta ajustável

Conferir no local • RRT/ART obrigatórias

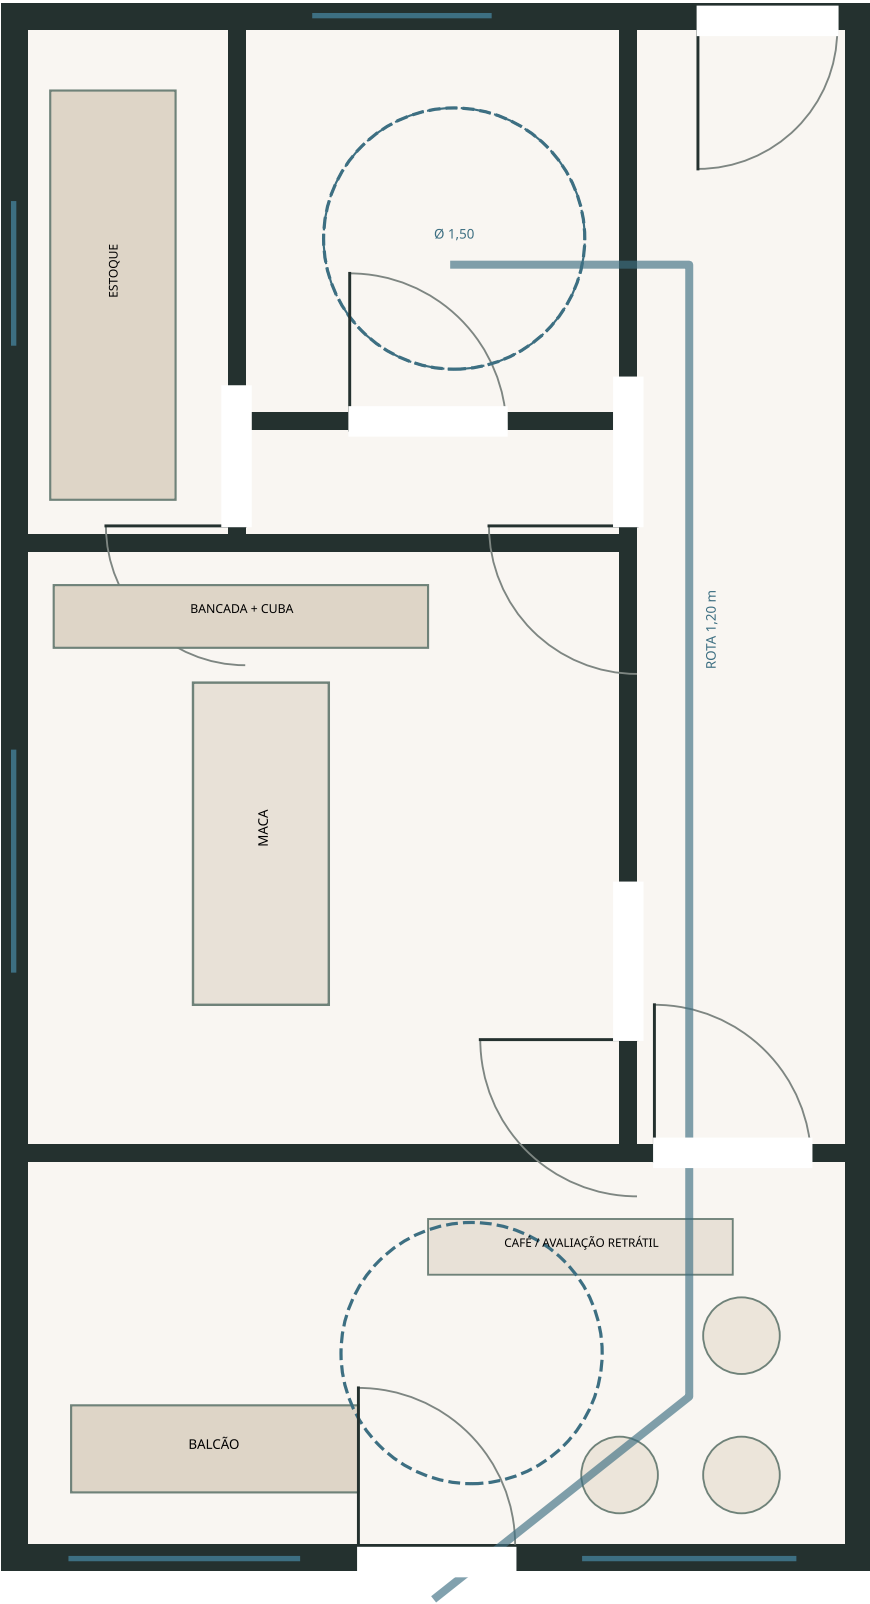

LUMINA

SKIN INTELLIGENCE

C-A03

ACESSIBILIDADE

Alternativa compacta — 5,00 × 9,00 m

ALTERNATIVA COMPACTA

Envoltória	5,00 × 9,00 m
Área bruta	45,00 m²
Operação	1 atendimento
Circulação	1,20 m
Implantação	Maior de 2027
Status	Comparativo


PARÂMETROS

Portas: vão livre ≥ 0,80 m. Rota: 1,20 m. Giros: Ø 1,50 m. Sanitário e balcão dependem de detalhamento e validação local.

Clínica Lumina Skin Intelligence

Alternativa compacta ajustável

Conferir no local • RRT/ART obrigatórias

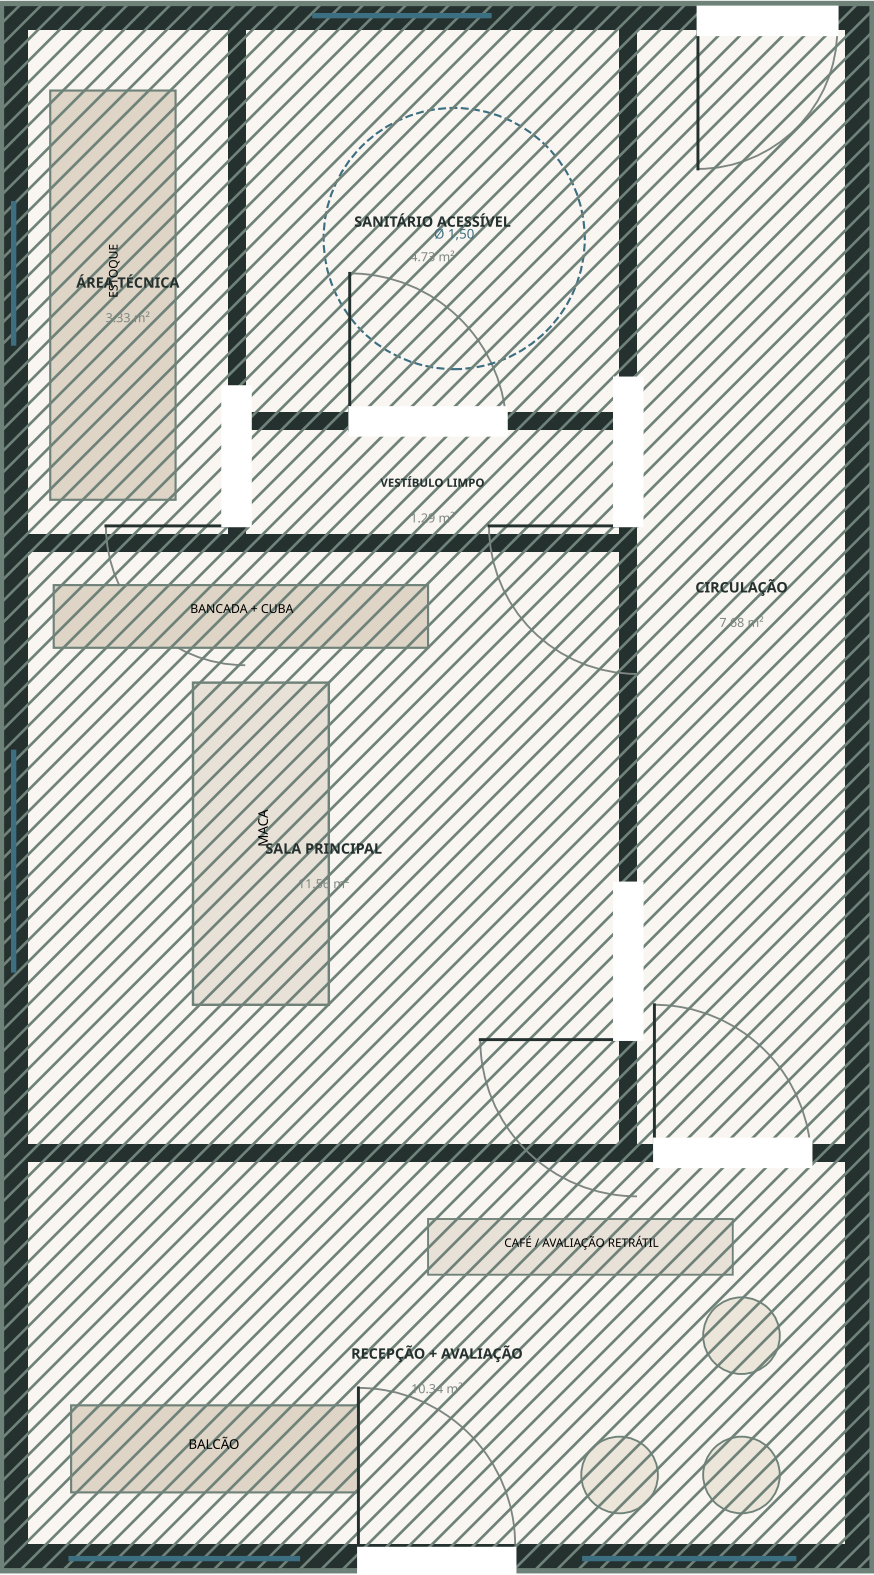

LUMINA

SKIN INTELLIGENCE

C-A04

CONSTRUÇÃO / INTERVENÇÃO

Alternativa compacta — 5,00 × 9,00 m

ALTERNATIVA COMPACTA

Envoltória	5,00 × 9,00 m
Área bruta	45,00 m²
Operação	1 atendimento
Circulação	1,20 m
Implantação	Maior de 2027
Status	Comparativo



INTERVENÇÃO

Módulo novo proposto. Sem demolição na hipótese. Interfaces com a casa, terreno, acessos e redes devem ser levantadas.

Clínica Lumina Skin Intelligence

Alternativa compacta ajustável

Conferir no local • RRT/ART obrigatórias

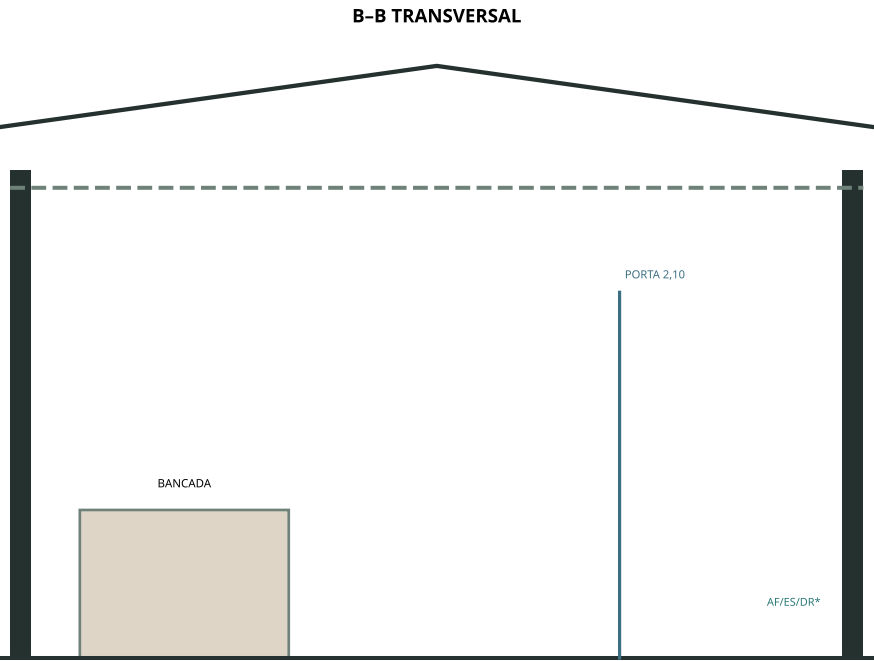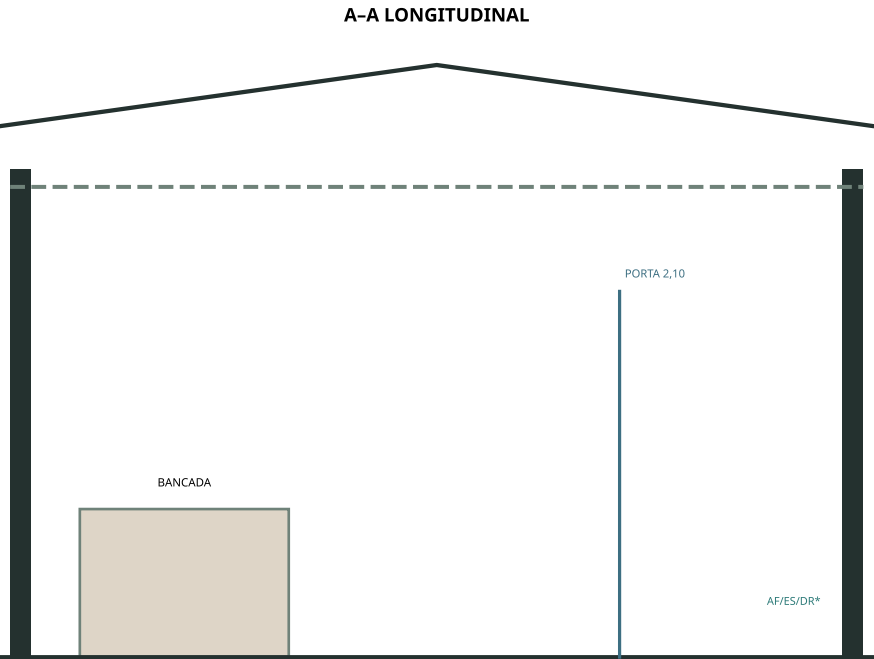

LUMINA

SKIN INTELLIGENCE

C-A05

CORTES ARQUITETÔNICOS

Longitudinal e transversal — alternativa 45 m²

ALTERNATIVA COMPACTA

Envoltória	5,00 × 9,00 m
Área bruta	45,00 m²
Operação	1 atendimento
Circulação	1,20 m
Implantação	Maior de 2027
Status	Comparativo


ALTURAS

Piso ±0,00. Forro +2,70 m. Cumeeira indicativa +3,40 m. Bancadas, portas, barras e instalações deverão ser detalhadas no executivo.

Clínica Lumina Skin Intelligence

Alternativa compacta ajustável

Conferir no local • RRT/ART obrigatórias

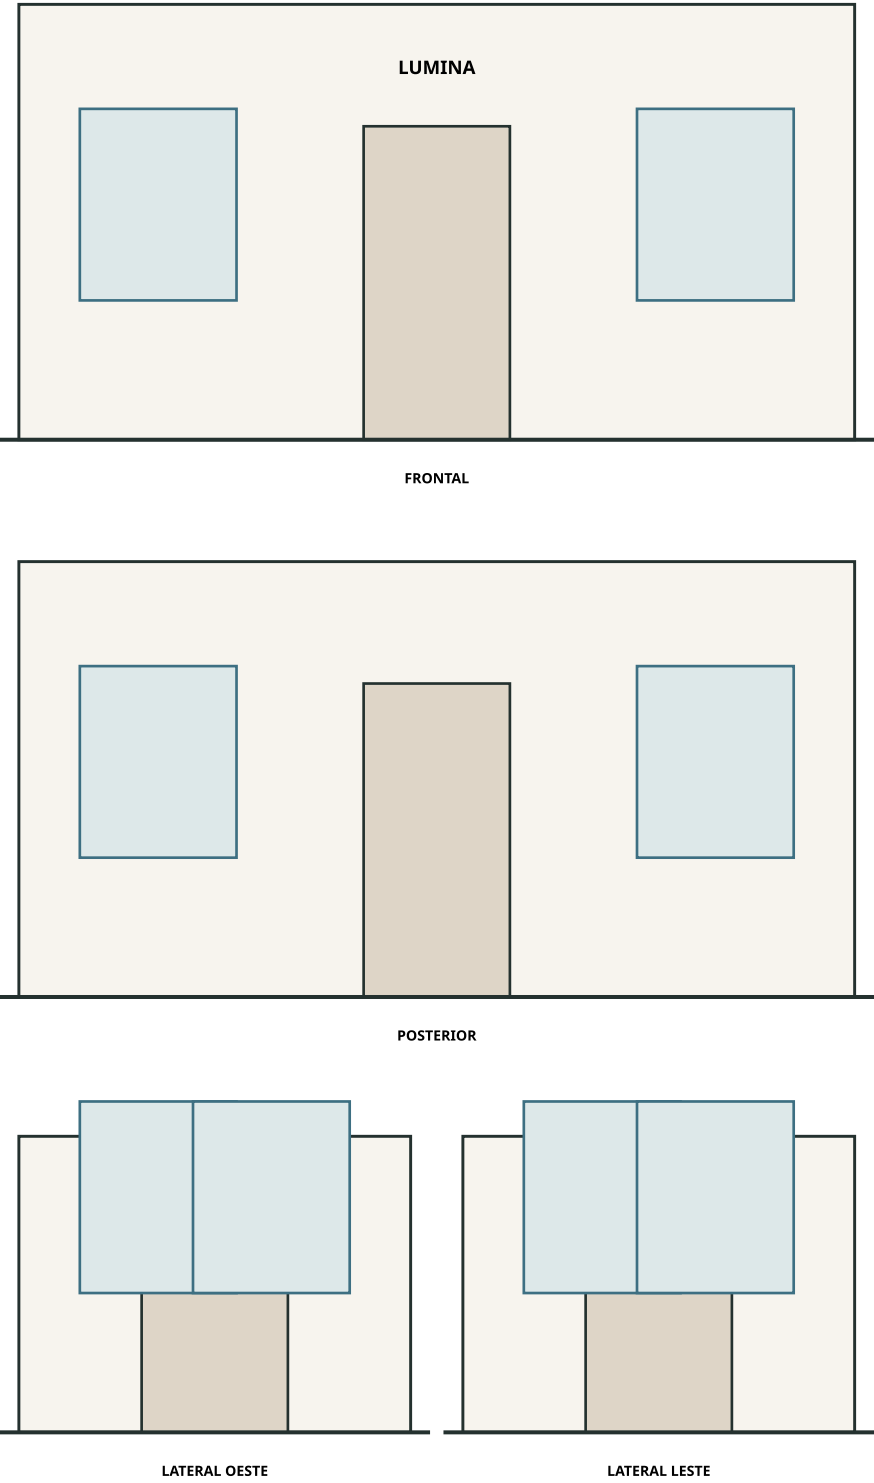

LUMINA

SKIN INTELLIGENCE

C-A06

FACHADAS

Frontal, posterior e laterais — alternativa compacta

ALTERNATIVA COMPACTA

Envoltória	5,00 × 9,00 m
Área bruta	45,00 m²
Operação	1 atendimento
Circulação	1,20 m
Implantação	Maior de 2027
Status	Comparativo

MATERIAIS

Reboco marfim, esquadrias grafite/champanhe, detalhe amadeirado, sinalização discreta e iluminação quente. Validar recuos e anúncios.

Clínica Lumina Skin Intelligence

Alternativa compacta ajustável

Conferir no local • RRT/ART obrigatórias

CÓD.	TIPO	DIMENSÃO	MATERIAL	OBSERVAÇÃO
P01-P04	Abrir	0,90 × 2,10	Laminado lavável	vão livre ≥ 0,80
P05	Correr	0,90 × 2,10	Alumínio/laminado	sanitário acessível
P06	Abrir	0,80 × 2,10	Laminado lavável	saída técnica
J01	Janela	1,30 × 1,10	Alumínio + vidro	recepção
J02	Janela	1,20 × 1,10	Alumínio + vidro	recepção
J03	Janela	1,25 × 1,10	Alumínio + vidro	sala
J04	Maxim-ar	0,80 × 0,60	Alumínio + vidro	apoio
J05	Maxim-ar	1,00 × 0,60	Alumínio + vidro	sanitário

LUMINA

SKIN INTELLIGENCE

C-A07

QUADRO DE ESQUADRIAS

Alternativa compacta — conferir no executivo


ALTERNATIVA COMPACTA

Envoltória	5,00 × 9,00 m
Área bruta	45,00 m²
Operação	1 atendimento
Circulação	1,20 m
Implantação	Maior de 2027
Status	Comparativo

Clínica Lumina Skin Intelligence

Alternativa compacta ajustável

Conferir no local • RRT/ART obrigatórias

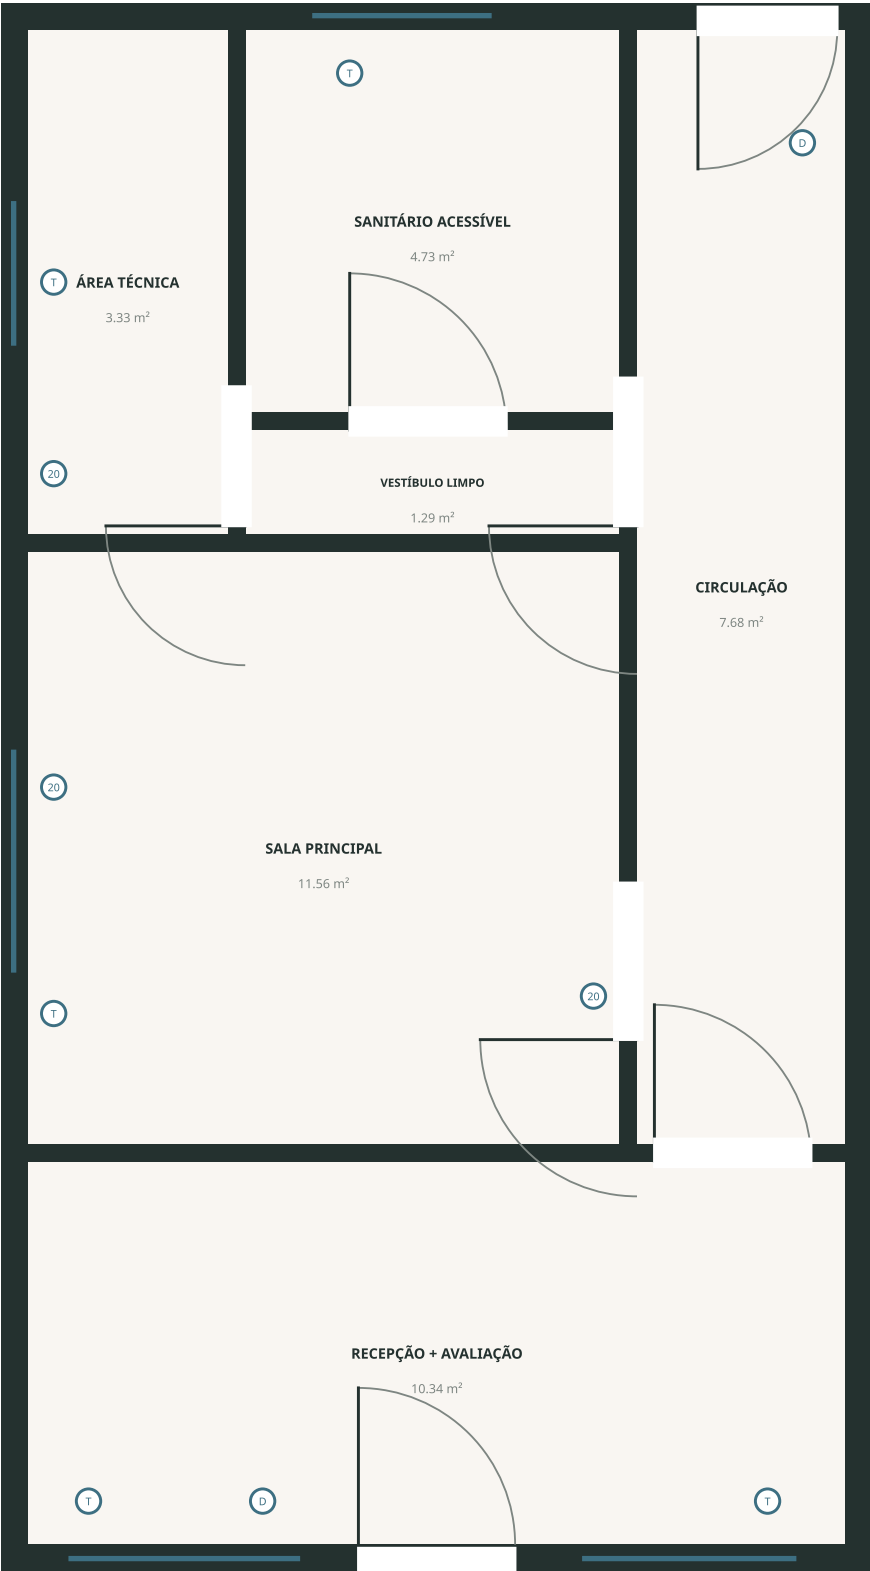

LUMINA

SKIN INTELLIGENCE

C-E01

ELÉTRICA E DADOS

Alternativa compacta — 5,00 × 9,00 m

ALTERNATIVA COMPACTA

Envoltória	5,00 × 9,00 m
Área bruta	45,00 m²
Operação	1 atendimento
Circulação	1,20 m
Implantação	Maior de 2027
Status	Comparativo

LEGENDA


T tomada geral
20 reserva dedicada*
D dados/rede

*Confirmar tensão, carga, DR, DPS, aterramento e plugue pelo manual.

Clínica Lumina Skin Intelligence

Alternativa compacta ajustável

Conferir no local • RRT/ART obrigatórias

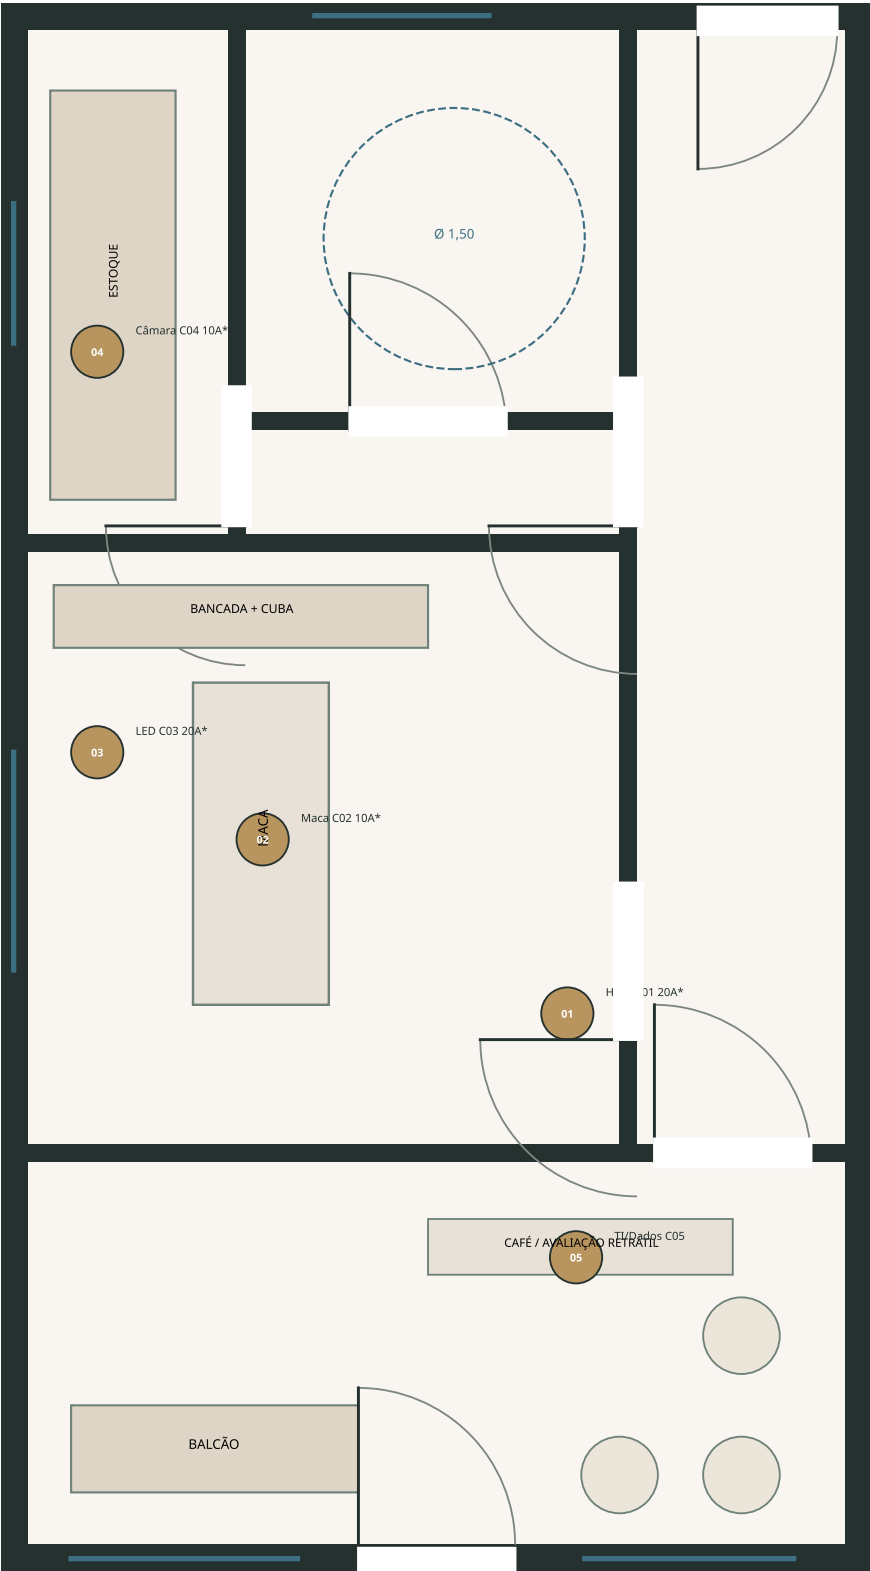

LUMINA

SKIN INTELLIGENCE

C-E02

PONTOS DE EQUIPAMENTOS

Alternativa compacta — 5,00 × 9,00 m

ALTERNATIVA COMPACTA

Envoltória	5,00 × 9,00 m
Área bruta	45,00 m²
Operação	1 atendimento
Circulação	1,20 m
Implantação	Maior de 2027
Status	Comparativo


RESERVAS

Cargas são apenas reservas de circuito. Confirmar potência, plugue, dados, dreno e ventilação pelos manuais antes da obra.

Clínica Lumina Skin Intelligence

Alternativa compacta ajustável

Conferir no local • RRT/ART obrigatórias

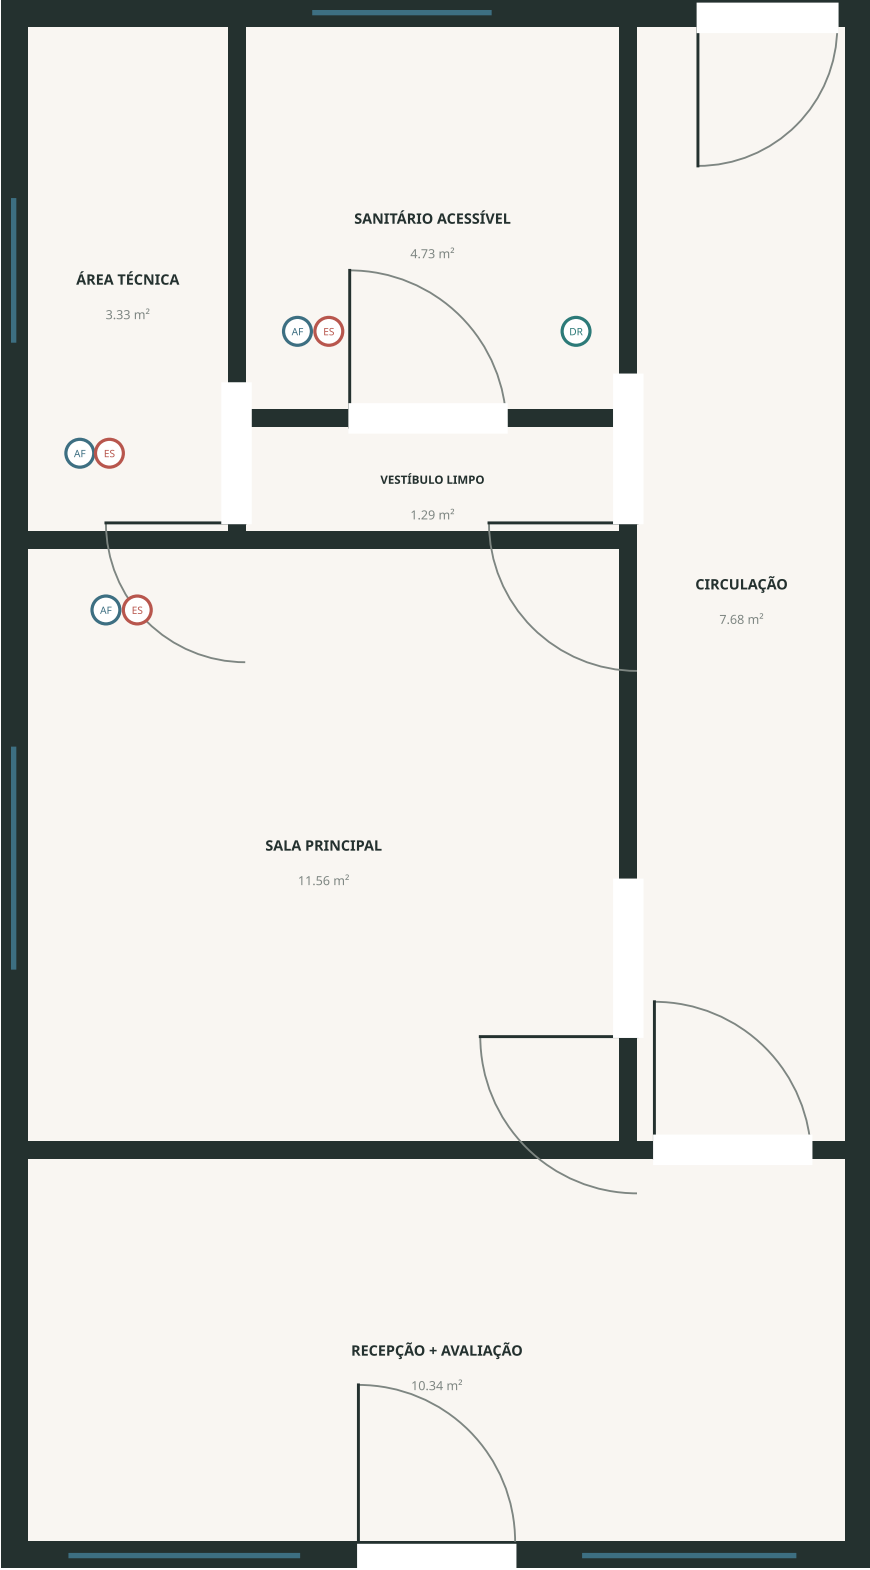

LUMINA

SKIN INTELLIGENCE

C-H01

HIDRÁULICA E SANITÁRIA

Alternativa compacta — 5,00 × 9,00 m

ALTERNATIVA COMPACTA

Envoltória	5,00 × 9,00 m
Área bruta	45,00 m²
Operação	1 atendimento
Circulação	1,20 m
Implantação	Maio de 2027
Status	Comparativo

LEGENDA


AF água fria
ES esgoto
DR dreno

Prumadas concentradas no fundo. Diâmetros, ventilação e declividades pelo projeto de arquitetura.

Clínica Lumina Skin Intelligence

Alternativa compacta ajustável

Conferir no local • RRT/ART obrigatórias

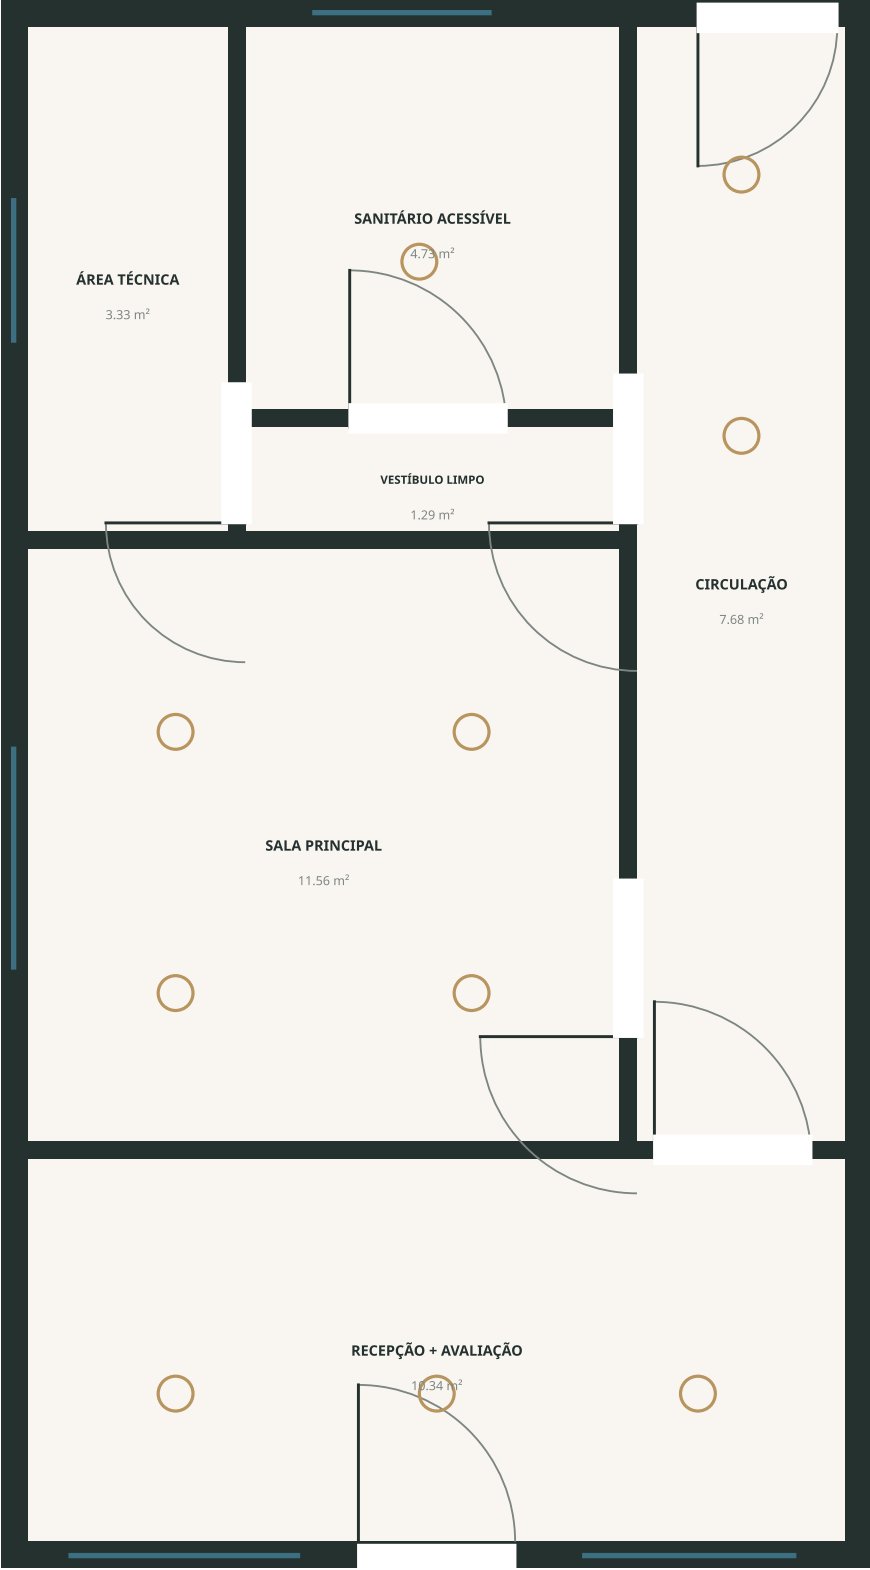

LUMINA

SKIN INTELLIGENCE

C-L01

FORRO E ILUMINAÇÃO

Alternativa compacta — 5,00 × 9,00 m

ALTERNATIVA COMPACTA

Envoltória	5,00 × 9,00 m
Área bruta	45,00 m²
Operação	1 atendimento
Circulação	1,20 m
Implantação	Maior de 2027
Status	Comparativo

DIRETRIZES

Luz acolhedora na recepção e luz clínica neutra na sala. Alto IRC na avaliação. Comandos independentes e sem ofuscamento.

Clínica Lumina Skin Intelligence

Alternativa compacta ajustável

Conferir no local • RRT/ART obrigatórias



LUMINA

SKIN INTELLIGENCE

C-M01

CLIMATIZAÇÃO E VENTILAÇÃO

Alternativa compacta — 5,00 × 9,00 m

ALTERNATIVA COMPACTA

Envoltória	5,00 × 9,00 m
Área bruta	45,00 m²
Operação	1 atendimento
Circulação	1,20 m
Implantação	Maio de 2027
Status	Comparativo


DIRETRIZES

Dimensionar carga térmica e renovação. Não direcionar jato sobre a maca. Prever drenos e manutenção.

Clínica Lumina Skin Intelligence

Alternativa compacta ajustável

Conferir no local • RRT/ART obrigatórias

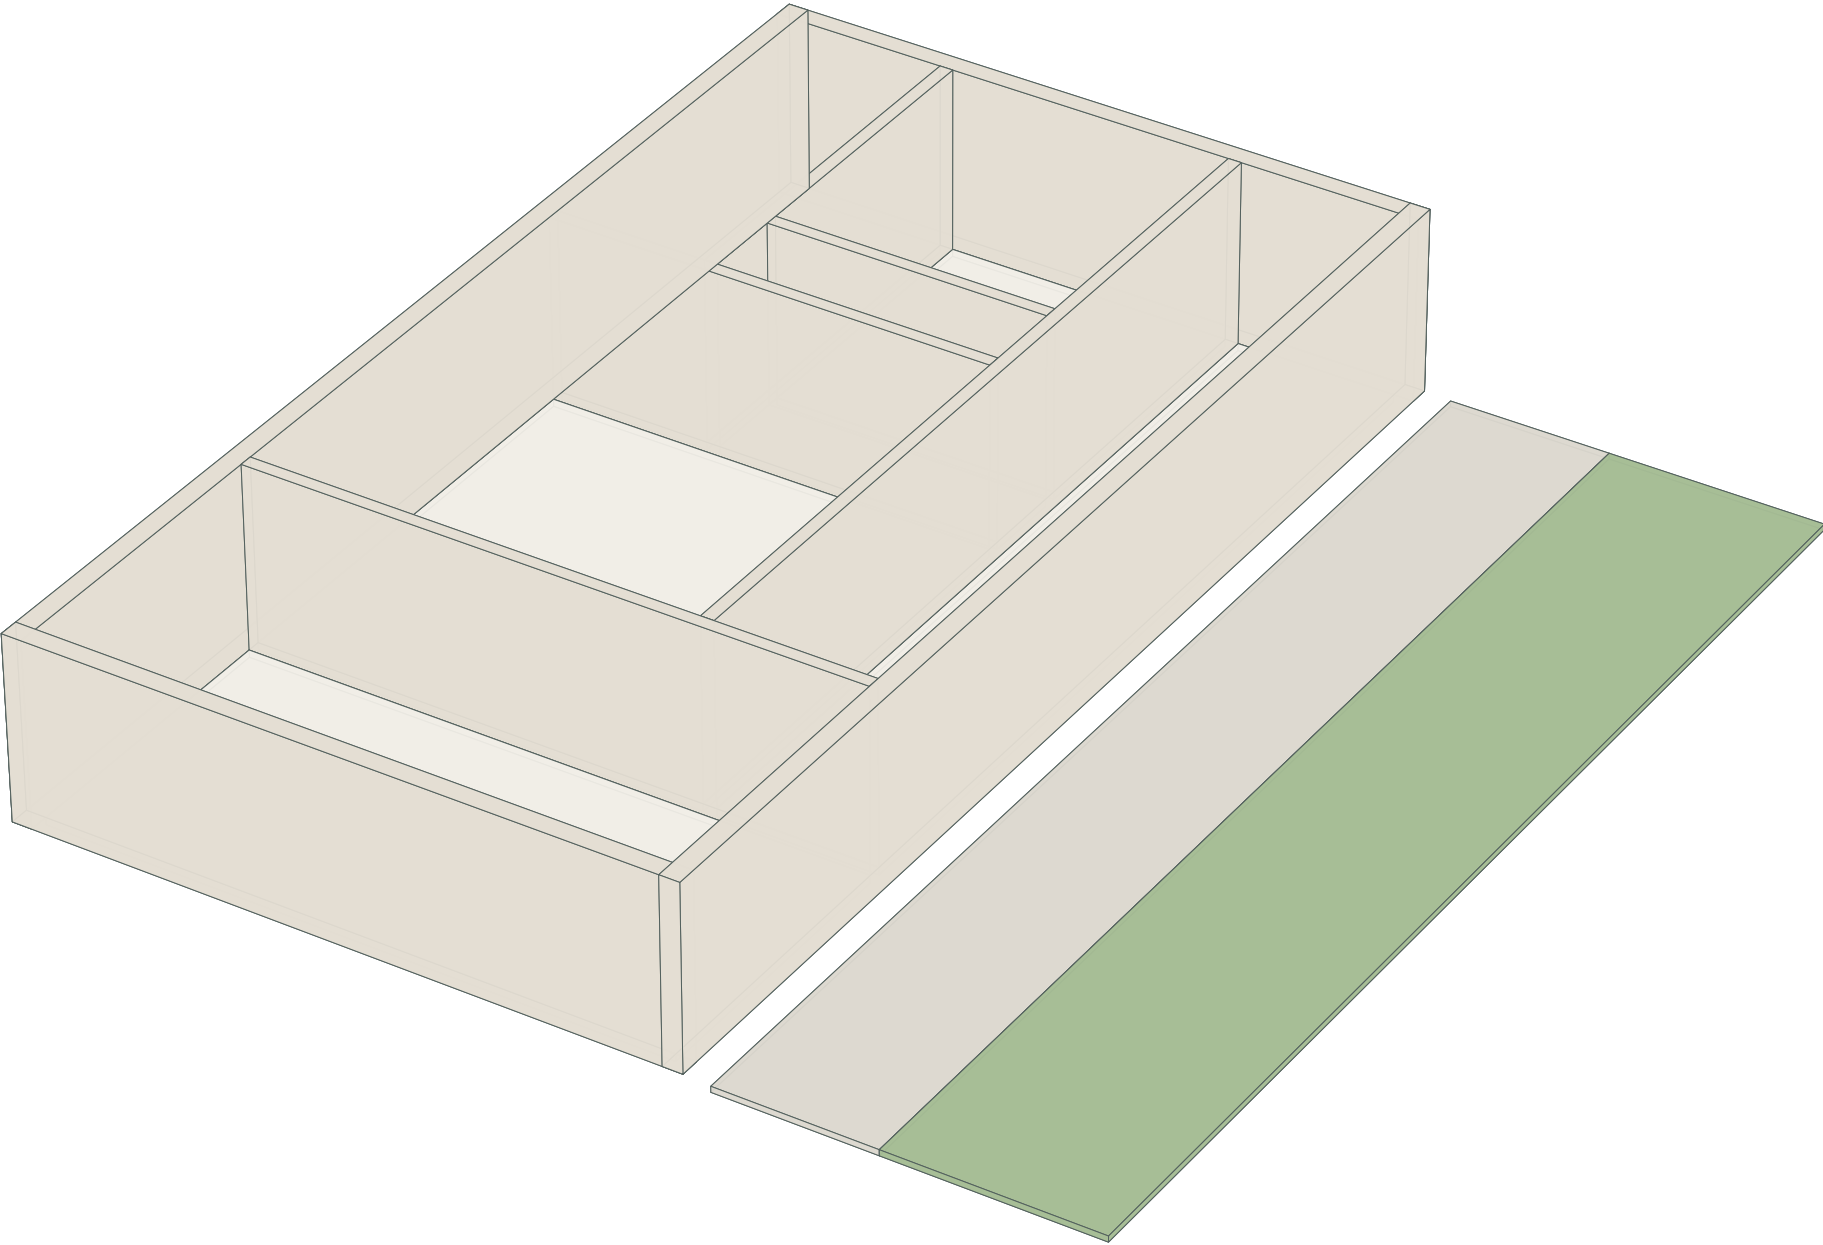

LUMINA

SKIN INTELLIGENCE

C-MQ01

MAQUETE 3D

Alternativa compacta + área externa

ALTERNATIVA COMPACTA

Envoltória	5,00 × 9,00 m
Área bruta	45,00 m²
Operação	1 atendimento
Circulação	1,20 m
Implantação	Maior de 2027
Status	Comparativo

Clínica Lumina Skin Intelligence

Alternativa compacta ajustável

Conferir no local • RRT/ART obrigatórias