


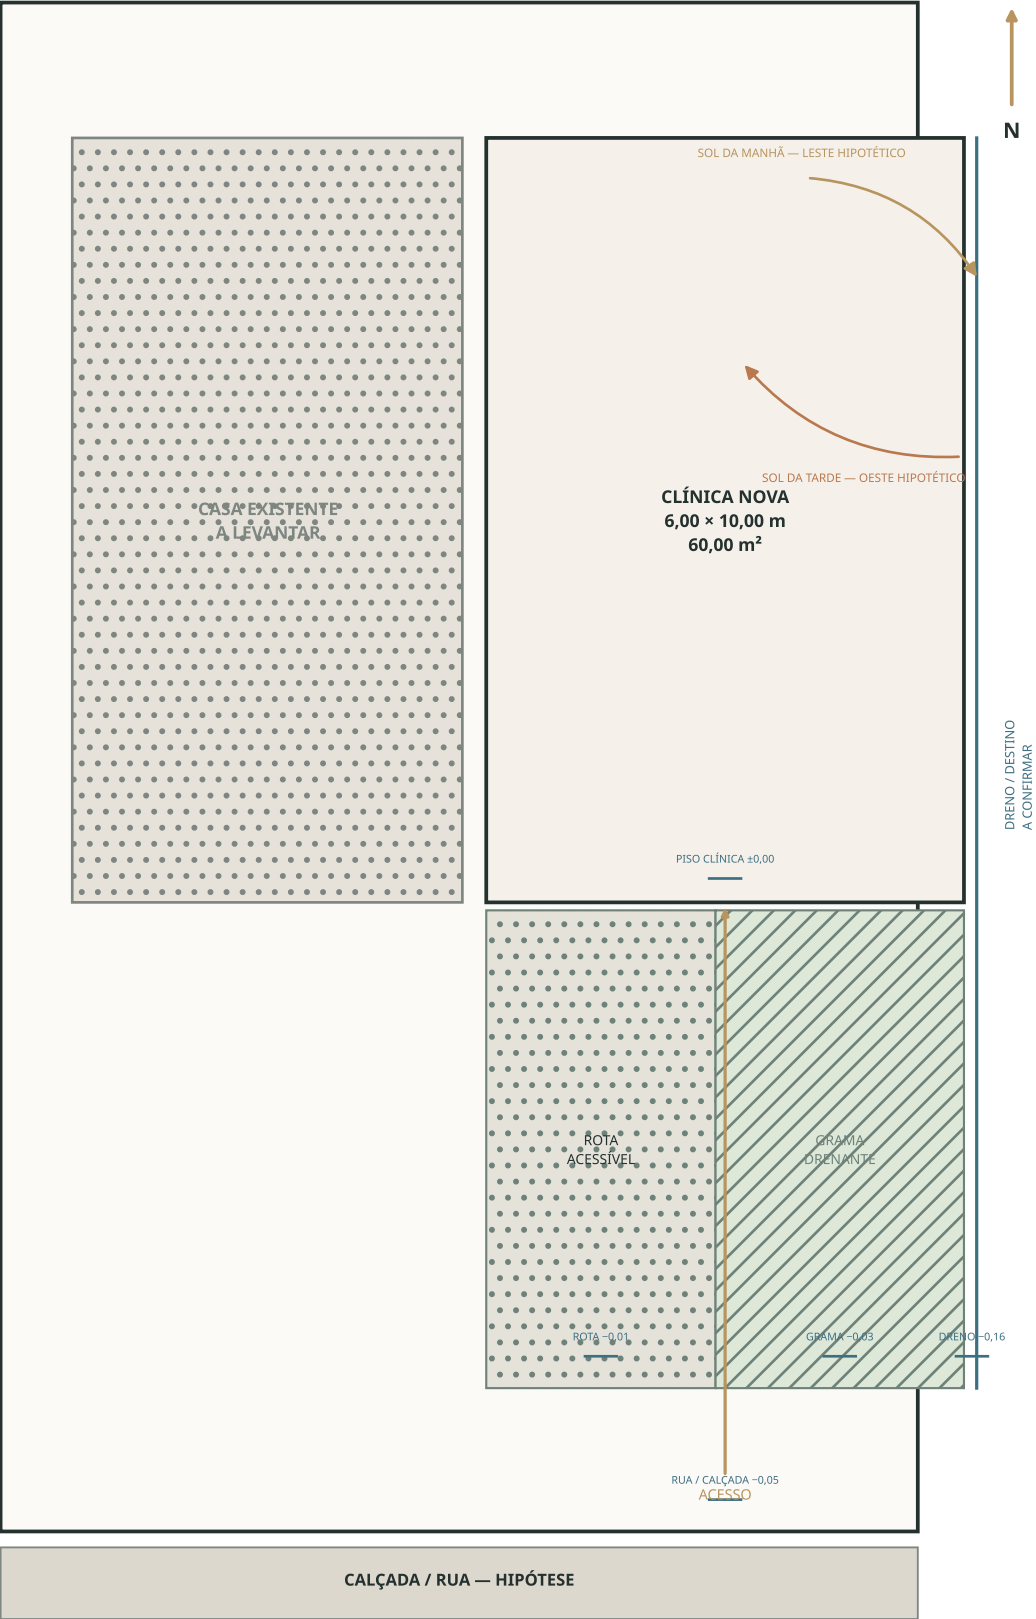

# LUMINA

SKIN INTELLIGENCE

## I-01

### IMPLANTAÇÃO BASE

Hipótese de lote 12,00 x 20,00 m; rua ao sul — substituir pelo levantamento real

#### DADOS DO ANTEPROJETO

|                |                   |
|----------------|-------------------|
| Envoltória     | 6,00 x 10,00 m    |
| Área bruta     | 60,00 m²          |
| Pavimento      | Térreo            |
| Escala gráfica | Indicativa        |
| Implantação    | Maior de 2027     |
| Status         | Estudo preliminar |


#### PENDÊNCIAS OBRIGATÓRIAS

- Medidas e matrícula do lote.
- Posição, estrutura e instalações da casa.
- Norte verdadeiro e insolação.
- Cotas de nível e solo.
- Recuos e código de obras.
- Ligação de água, esgoto e energia.
- Destino legal das águas pluviais.

#### Clínica Lumina Skin Intelligence

Anteprojeto-base ajustável

Conferir no local • Aprovação e RRT/ART obrigatórias

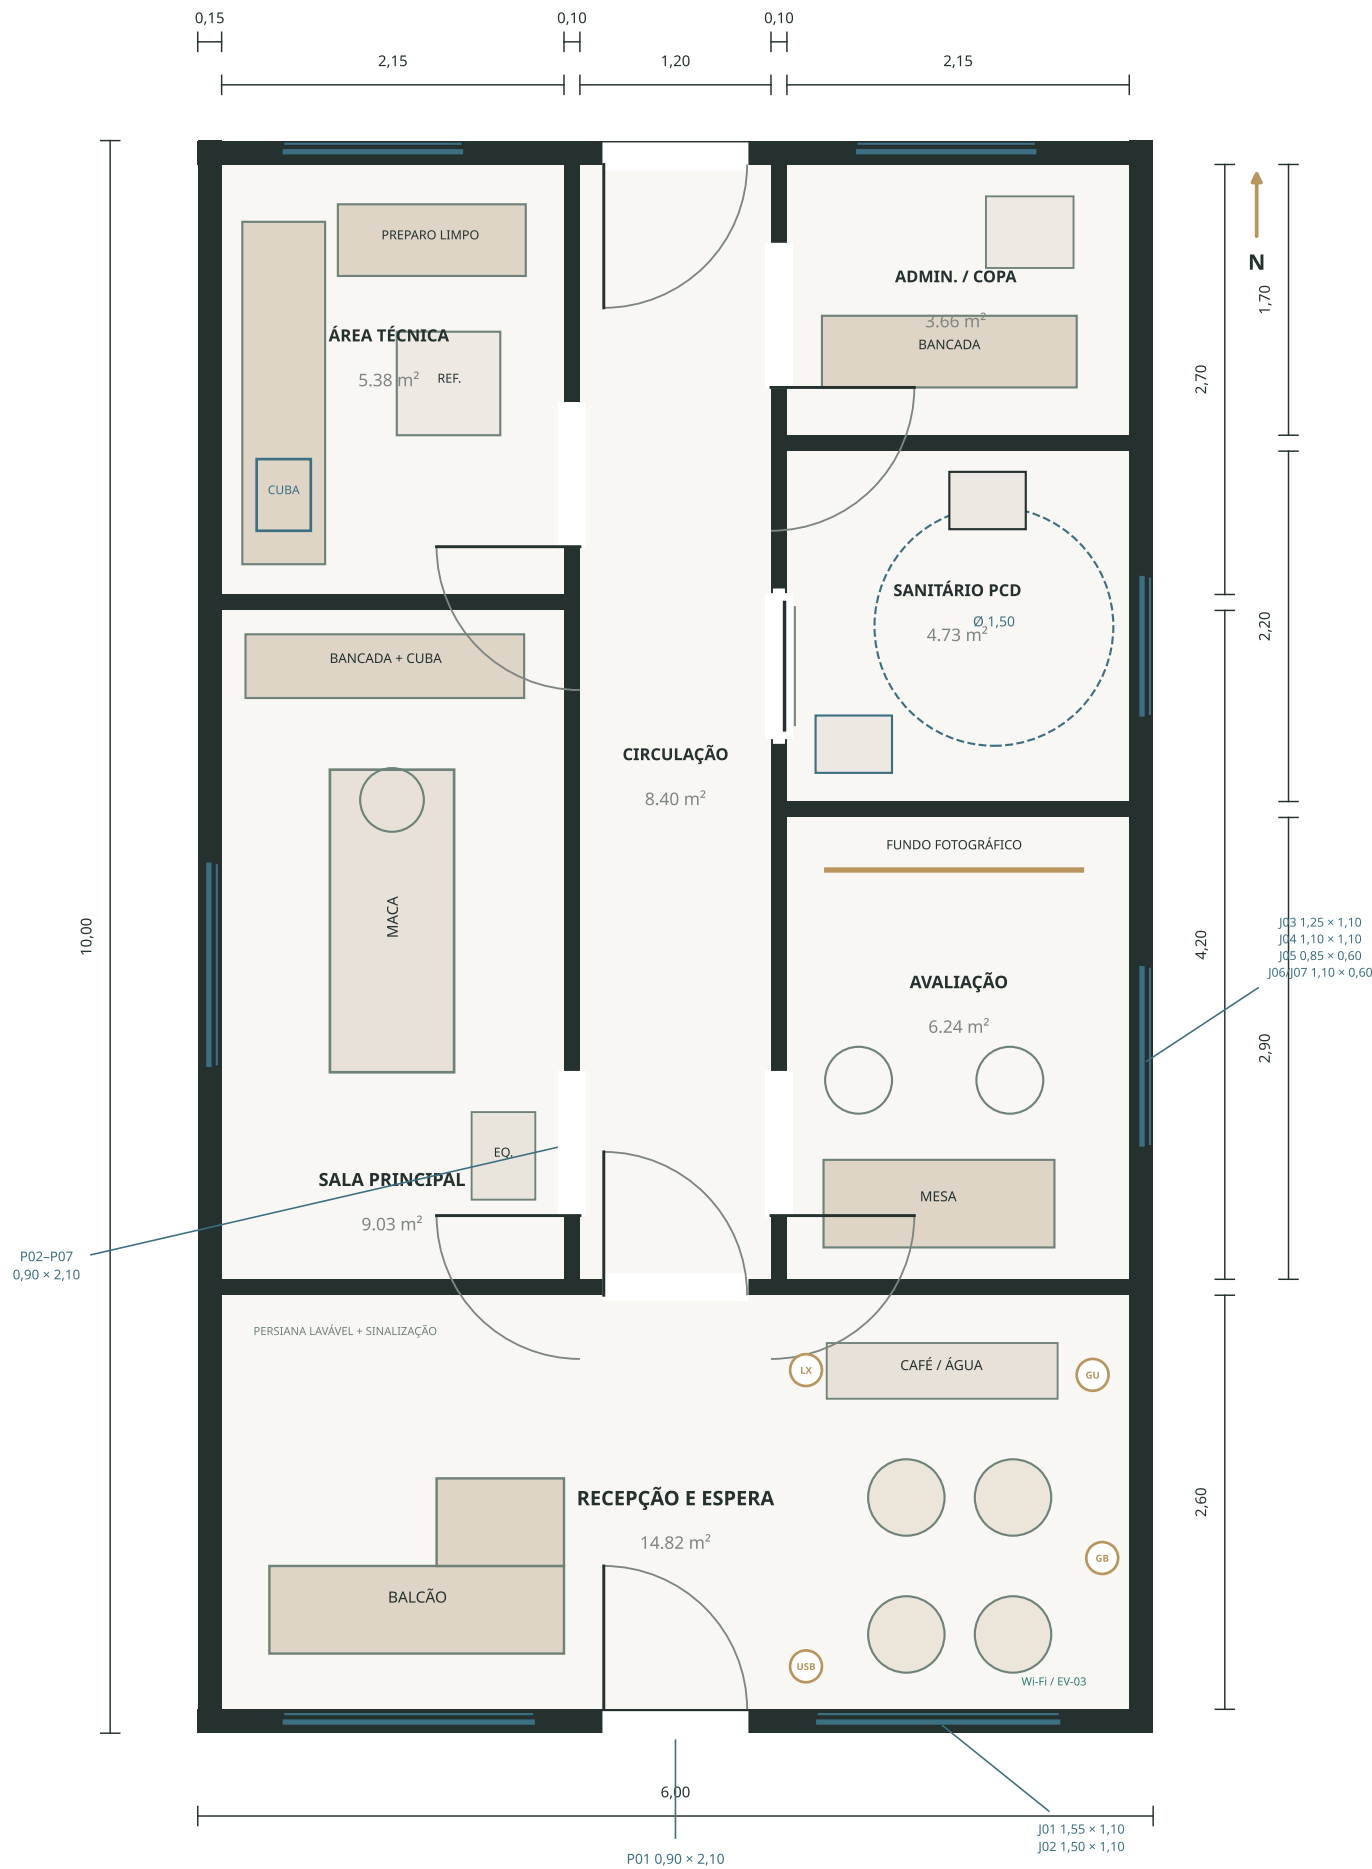

# LUMINA

SKIN INTELLIGENCE

A-01

## PLANTA BAIXA COTADA

Layout, mobiliário e quadro de áreas — estudo preliminar

### DADOS DO ANTEPROJETO

|                |                   |
|----------------|-------------------|
| Envoltória     | 6,00 × 10,00 m    |
| Área bruta     | 60,00 m²          |
| Pavimento      | Térreo            |
| Escala gráfica | Indicativa        |
| Implantação    | Maio de 2027      |
| Status         | Estudo preliminar |


### QUADRO DE ÁREAS

|                        |          |
|------------------------|----------|
| Recepção e espera      | 14.82 m² |
| Sala principal         | 9.03 m²  |
| Circulação clínica     | 8.40 m²  |
| Avaliação / fotografia | 6.23 m²  |
| Sanitário acessível    | 4.73 m²  |
| Administração / copa   | 3.65 m²  |
| Área técnica / estoque | 5.80 m²  |

### Clínica Lumina Skin Intelligence

Anteprojeto-base ajustável

Conferir no local • Aprovação e RRT/ART obrigatórias

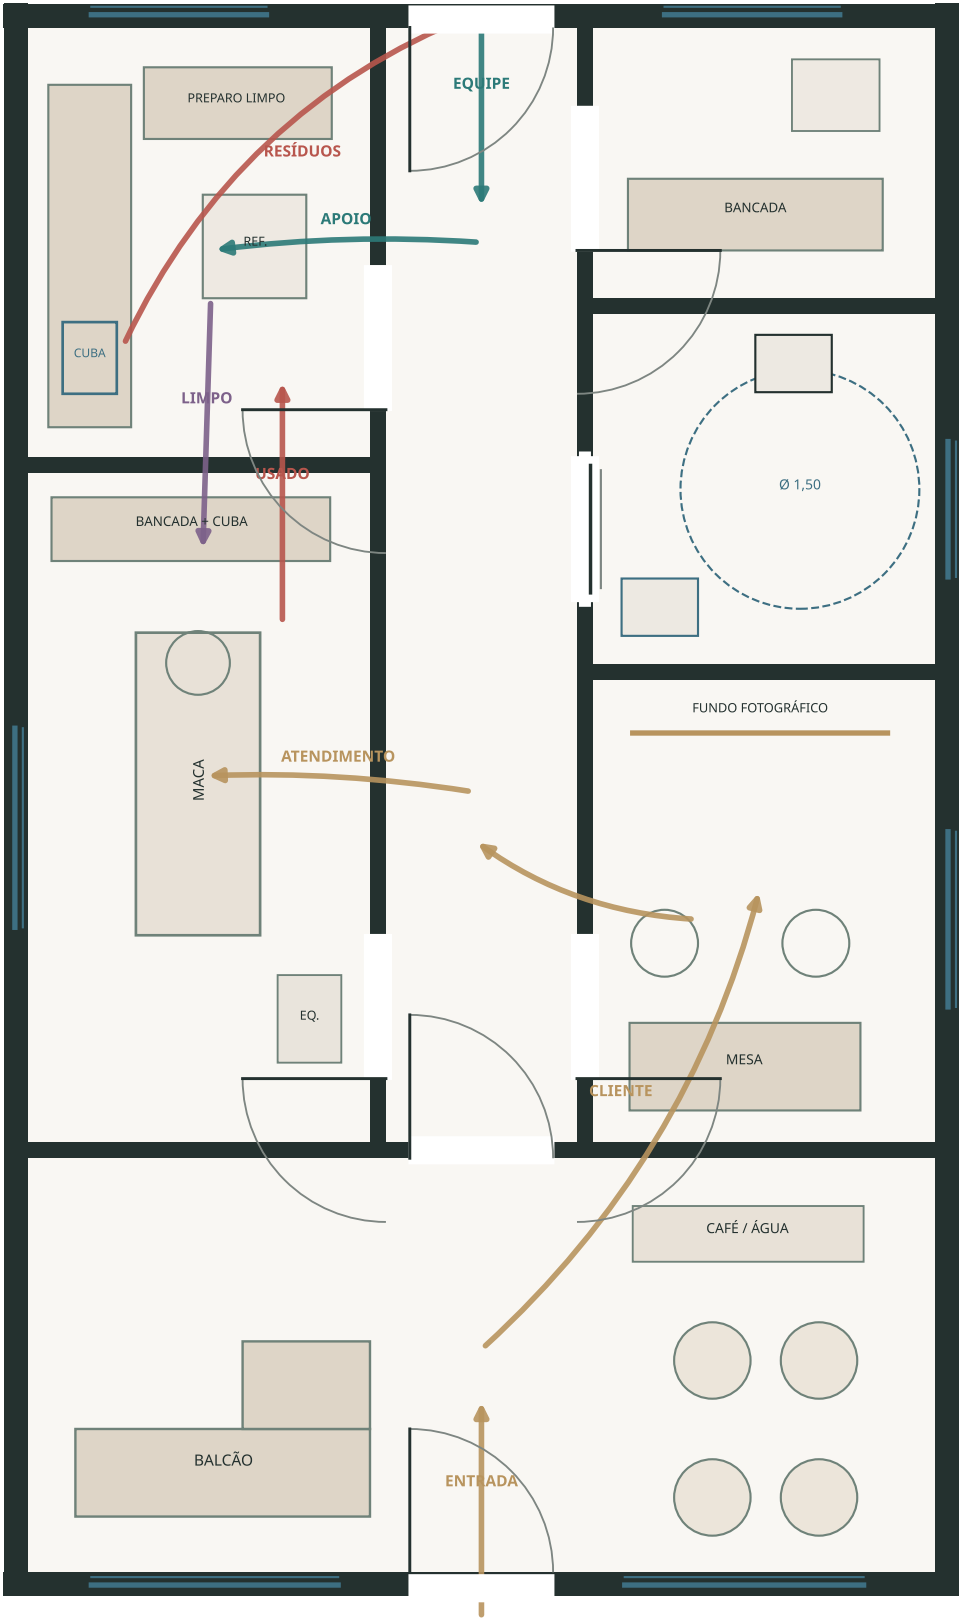

— Cliente — Material limpo  
— Equipe — Material usado / resíduos

# LUMINA

SKIN INTELLIGENCE

A-02

## FLUXOS E SETORIZAÇÃO

Público, equipe, material limpo e resíduos

### DADOS DO ANTEPROJETO

|                |                   |
|----------------|-------------------|
| Envoltória     | 6,00 × 10,00 m    |
| Área bruta     | 60,00 m²          |
| Pavimento      | Térreo            |
| Escala gráfica | Indicativa        |
| Implantação    | Maio de 2027      |
| Status         | Estudo preliminar |


### CRITÉRIOS

- Público não acessa apoio técnico.
- Material limpo e usado não ocupam a mesma bancada simultaneamente.
- Resíduos saem preferencialmente pelo fundo.
- Circulação central permanece desobstruída.

### Clínica Lumina Skin Intelligence

Anteprojeto-base ajustável

Conferir no local • Aprovação e RRT/ART obrigatórias

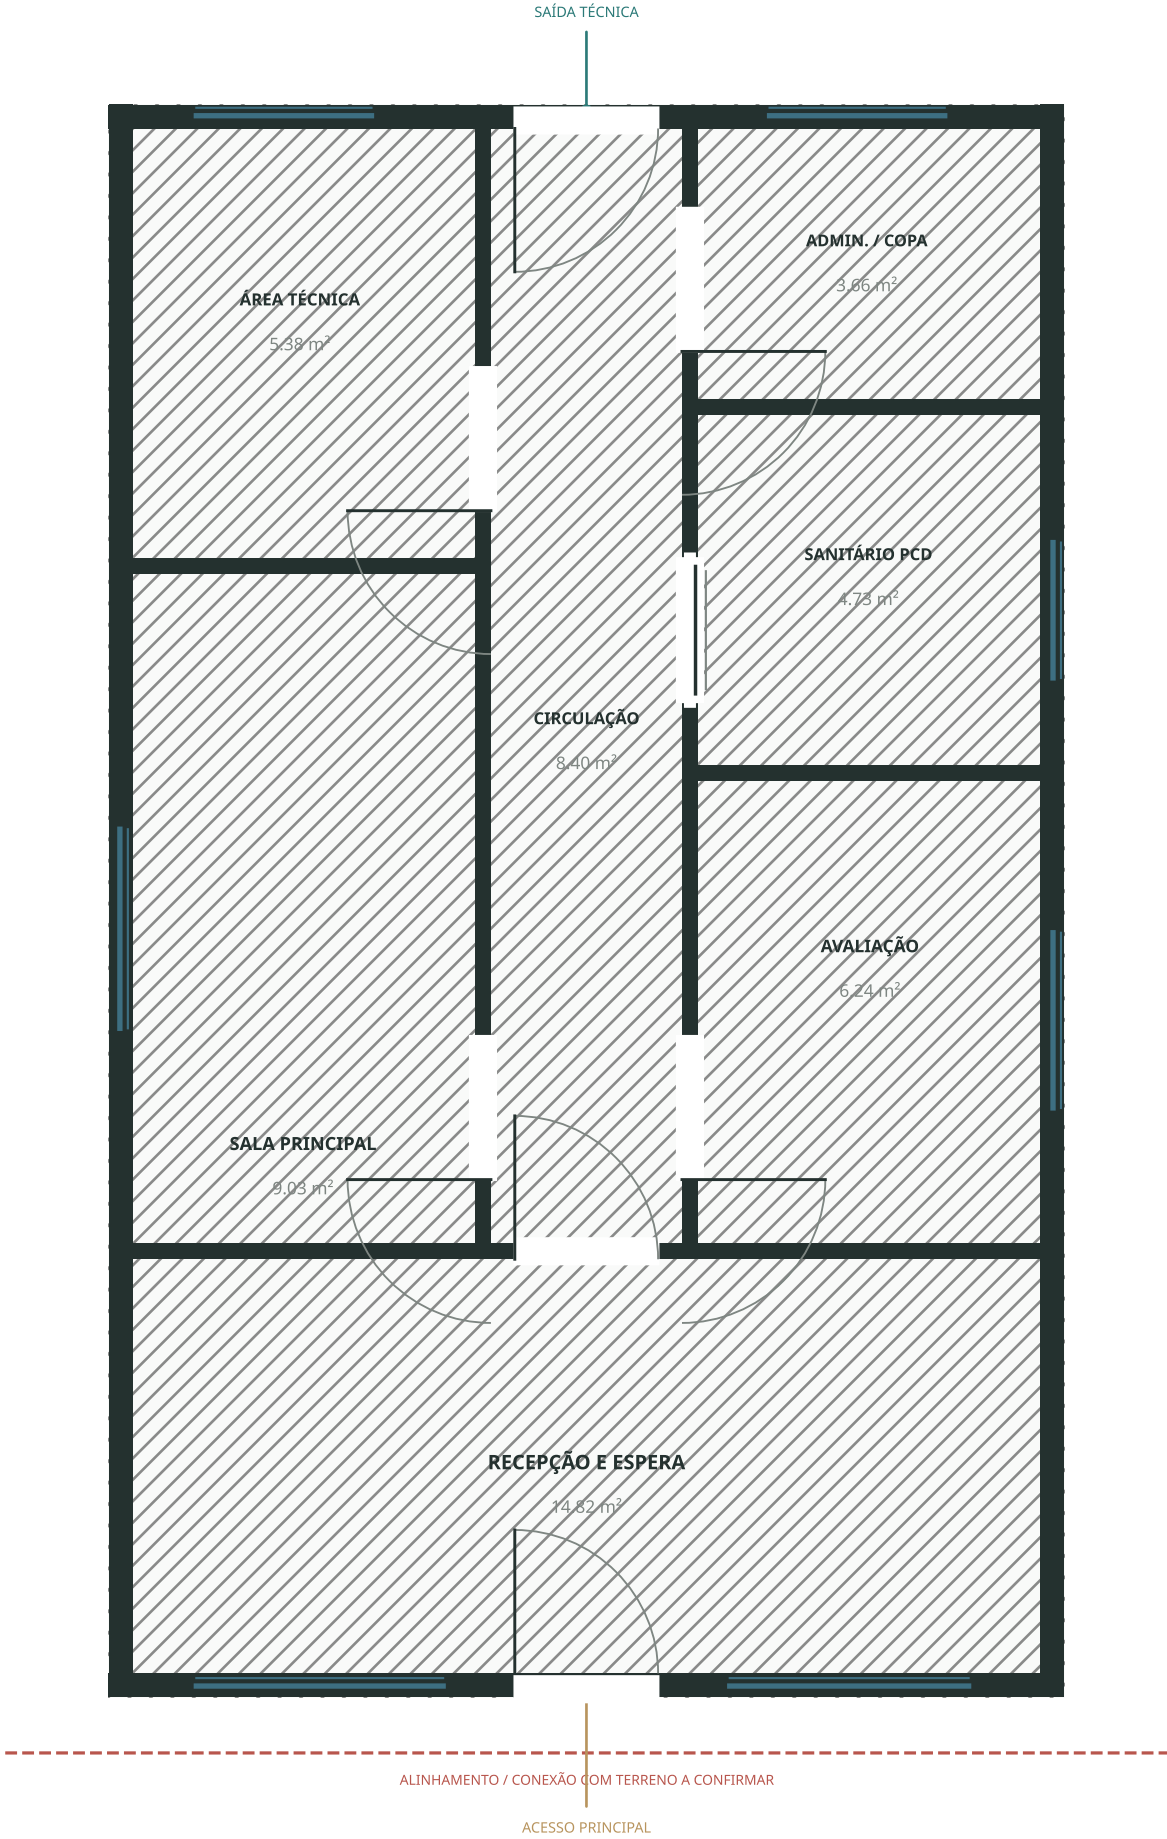

# LUMINA

SKIN INTELLIGENCE

A-04

## CONSTRUÇÃO / INTERVENÇÃO

Módulo novo independente; interfaces com a casa e o terreno a levantar

### DADOS DO ANTEPROJETO

|                |                   |
|----------------|-------------------|
| Envoltória     | 6,00 × 10,00 m    |
| Área bruta     | 60,00 m²          |
| Pavimento      | Térreo            |
| Escala gráfica | Indicativa        |
| Implantação    | Maio de 2027      |
| Status         | Estudo preliminar |

### LEGENDA DE INTERVENÇÃO



Hachura verde: área nova proposta.  
Paredes escuras: vedação nova.  
Linha vermelha: interface a levantar.  
Azul: esquadrias novas.

Não há demolição prevista nesta hipótese. Se a clínica for anexada ou ocupar construção existente, produzir levantamento e prancha específica “existente / demolir / construir” antes da obra.

### Clínica Lumina Skin Intelligence

Anteprojeto-base ajustável

Conferir no local • Aprovação e RRT/ART obrigatórias

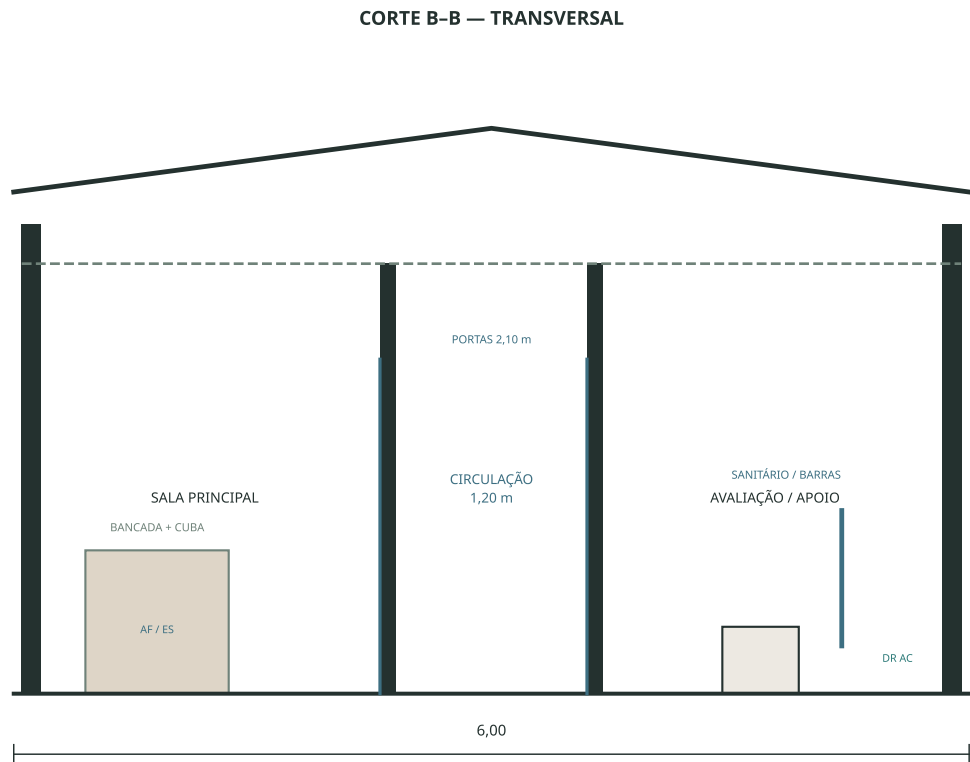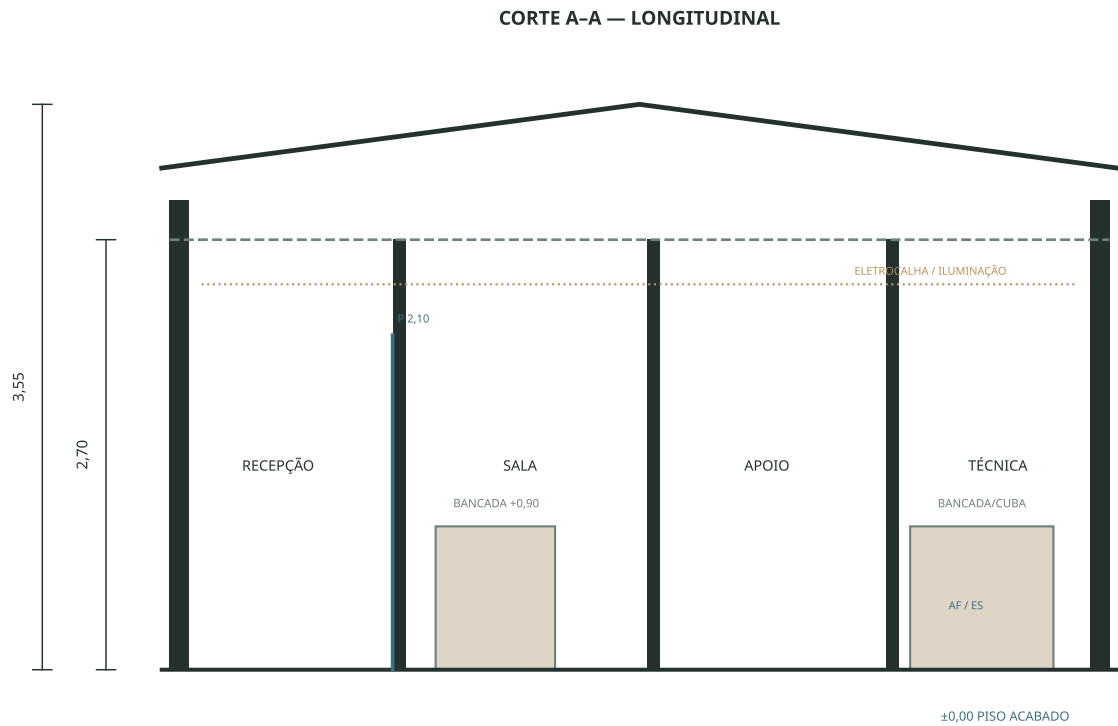

# LUMINA

SKIN INTELLIGENCE

## A-05

## CORTES ARQUITETÔNICOS

Cortes A-A e B-B; alturas e fundações a confirmar no projeto executivo

### DADOS DO ANTEPROJETO

|                |                   |
|----------------|-------------------|
| Envoltória     | 6,00 × 10,00 m    |
| Área bruta     | 60,00 m²          |
| Pavimento      | Térreo            |
| Escala gráfica | Indicativa        |
| Implantação    | Maio de 2027      |
| Status         | Estudo preliminar |

### ALTURAS INDICATIVAS


Piso acabado: ±0,00.  
Forro: +2,70 m.  
Cumeeira indicativa: +3,55 m.  
Cobertura leve isolada.

Validar estrutura, inclinação, pé-direito, impermeabilização, níveis externos e rota acessível no projeto executivo.


### Clínica Lumina Skin Intelligence

Anteprojeto-base ajustável


Conferir no local • Aprovação e RRT/ART obrigatórias

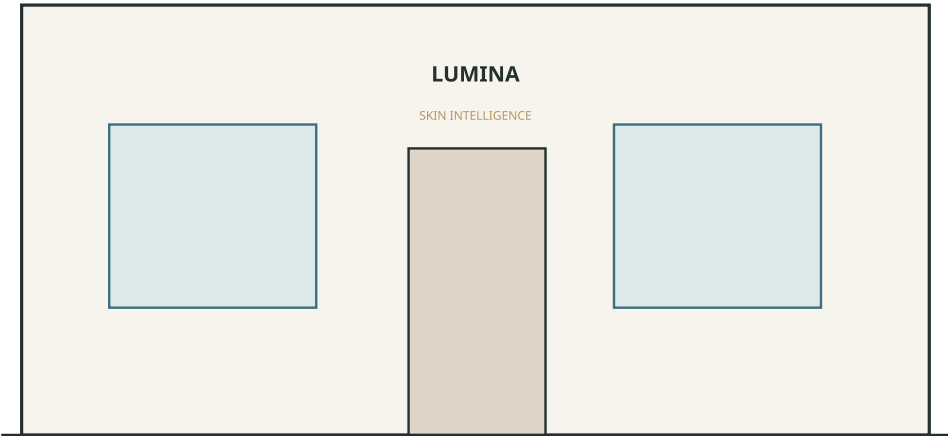

FACHADA FRONTAL — SUL HIPOTÉTICO

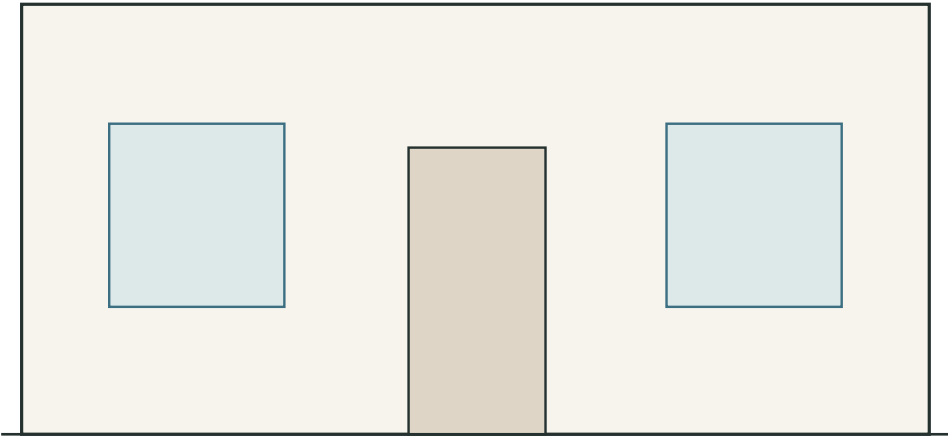

FACHADA POSTERIOR — NORTE HIPOTÉTICO

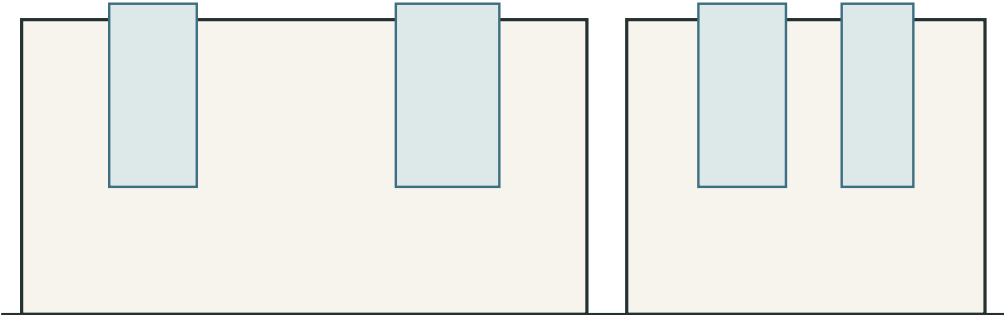

LATERAL OESTE — ESQUEMÁTICA

LATERAL LESTE — ESQUEMÁTICA

# LUMINA

SKIN INTELLIGENCE

A-06

## FACHADAS

Composição conceitual, materiais e sinalização — ajustar à implantação e legislação local

### DADOS DO ANTEPROJETO

|                |                   |
|----------------|-------------------|
| Envoltória     | 6,00 × 10,00 m    |
| Área bruta     | 60,00 m²          |
| Pavimento      | Térreo            |
| Escala gráfica | Indicativa        |
| Implantação    | Maio de 2027      |
| Status         | Estudo preliminar |

### PALETA E MATERIAIS

- Reboco liso em marfim quente.
- Esquadrias em champanhe/grafite.
- Detalhes verticais amadeirados.
- Letreiro retroiluminado indireto.
- Luz quente de acolhimento.
- Rodapé externo mineral escuro.
- Marquise e drenagem a dimensionar.

A fachada final depende de recuos, visibilidade, orientação solar e regra municipal de anúncios.

### Clínica Lumina Skin Intelligence

Anteprojeto-base ajustável

Conferir no local • Aprovação e RRT/ART obrigatórias



| CÓD.    | TIPO     | DIMENSÃO (m) | MATERIAL / ACABAMENTO    | OBSERVAÇÃO                 |
|---------|----------|--------------|--------------------------|----------------------------|
| P01     | Abrir    | 0,90 × 2,10  | Madeira/laminado lavável | Entrada; vão livre ≥ 0,80  |
| P02-P05 | Abrir    | 0,90 × 2,10  | Laminado lavável         | Salas; ferragem resistente |
| P06     | Correr   | 0,90 × 2,10  | Alumínio/laminado        | Sanitário acessível        |
| P07     | Abrir    | 0,90 × 2,10  | Laminado lavável         | Saída técnica              |
| J01     | Janela   | 1,55 × 1,10  | Alumínio + vidro         | Recepção; peitoril 1,00    |
| J02     | Janela   | 1,50 × 1,10  | Alumínio + vidro         | Recepção; peitoril 1,00    |
| J03     | Janela   | 1,25 × 1,10  | Alumínio + vidro         | Sala; peitoril 1,00        |
| J04     | Janela   | 1,10 × 1,10  | Alumínio + vidro         | Avaliação; peitoril 1,00   |
| J05     | Maxim-ar | 0,85 × 0,60  | Alumínio + vidro         | Sanitário; peitoril 1,60   |
| J06/J07 | Maxim-ar | 1,10 × 0,60  | Alumínio + vidro         | Apoio; peitoril 1,60       |

# LUMINA

SKIN INTELLIGENCE

A-07

## QUADRO DE ESQUADRIAS

Portas e janelas do anteprojeto; conferir medidas no executivo

### DADOS DO ANTEPROJETO

|                |                   |
|----------------|-------------------|
| Envoltória     | 6,00 × 10,00 m    |
| Área bruta     | 60,00 m²          |
| Pavimento      | Térreo            |
| Escala gráfica | Indicativa        |
| Implantação    | Maio de 2027      |
| Status         | Estudo preliminar |

### CRITÉRIOS

Ferragens sem arestas, superfícies laváveis, maçanetas acessíveis, vedações íntegras e telas quando exigidas. Confirmar ventilação, insolação, privacidade, segurança, sentido de abertura e resistência ao fogo no executivo.

### Clínica Lumina Skin Intelligence

Anteprojeto-base ajustável

Conferir no local • Aprovação e RRT/ART obrigatórias

D1 — BANCADA CLÍNICA + CUBA

Tampo não poroso com frontão

Cuba sem frestas e torneira clínica

Armário suspenso ou rodapé recuado

Selante sanitário compatível

Pontos AF/ES e inspeção

D2 — RODAPÉ E ENCONTRO DE PISO

Piso contínuo antiderrapante

Rodapé arredondado/lavável

Parede lisa e resistente

Junta selada e inspecionável

Impermeabilização em áreas molhadas

D3 — SANITÁRIO ACESSÍVEL

Reforço interno para barras

Barra e fixação estruturais

Bacia e lavatório acessíveis

Porta de correr 0,90 m

Giro Ø 1,50 m e alarme a validar

D4 — GRAMA + DRENO + ROTA

Grama sintética perfurada

Regularização drenante

Base granular + geotêxtil

Dreno linear inspecionável

Piso firme permeável sem ressalto

LUMINA

SKIN INTELLIGENCE

A-08

DETALHES CONSTRUTIVOS

Detalhes conceituais; materiais e fixações a especificar no executivo

DADOS DO ANTEPROJETO

Envoltória

6,00 × 10,00 m

Área bruta

60,00 m²

Pavimento

Térreo

Escala gráfica

Indicativa

Implantação

Maio de 2027

Status

Estudo preliminar

ANTES DE EXECUTAR



Produzir amostras, fichas técnicas, paginação, detalhes de impermeabilização, reforços, juntas, fixações e compatibilidade química. Fotografar instalações antes de fechar paredes e pisos. Submeter detalhes ao arquiteto/engenheiro e à Vigilância local.

Clínica Lumina Skin Intelligence

Anteprojeto-base ajustável

Conferir no local • Aprovação e RRT/ART obrigatórias



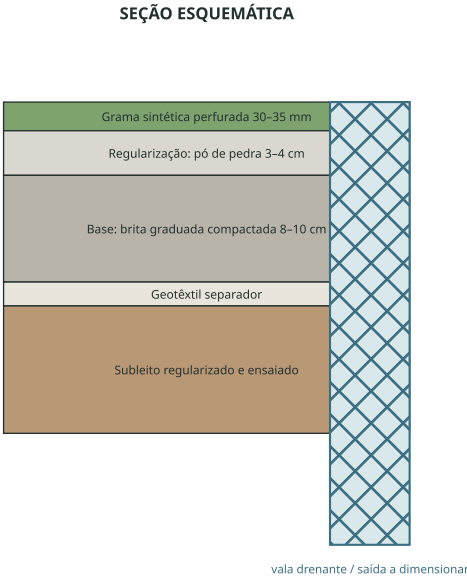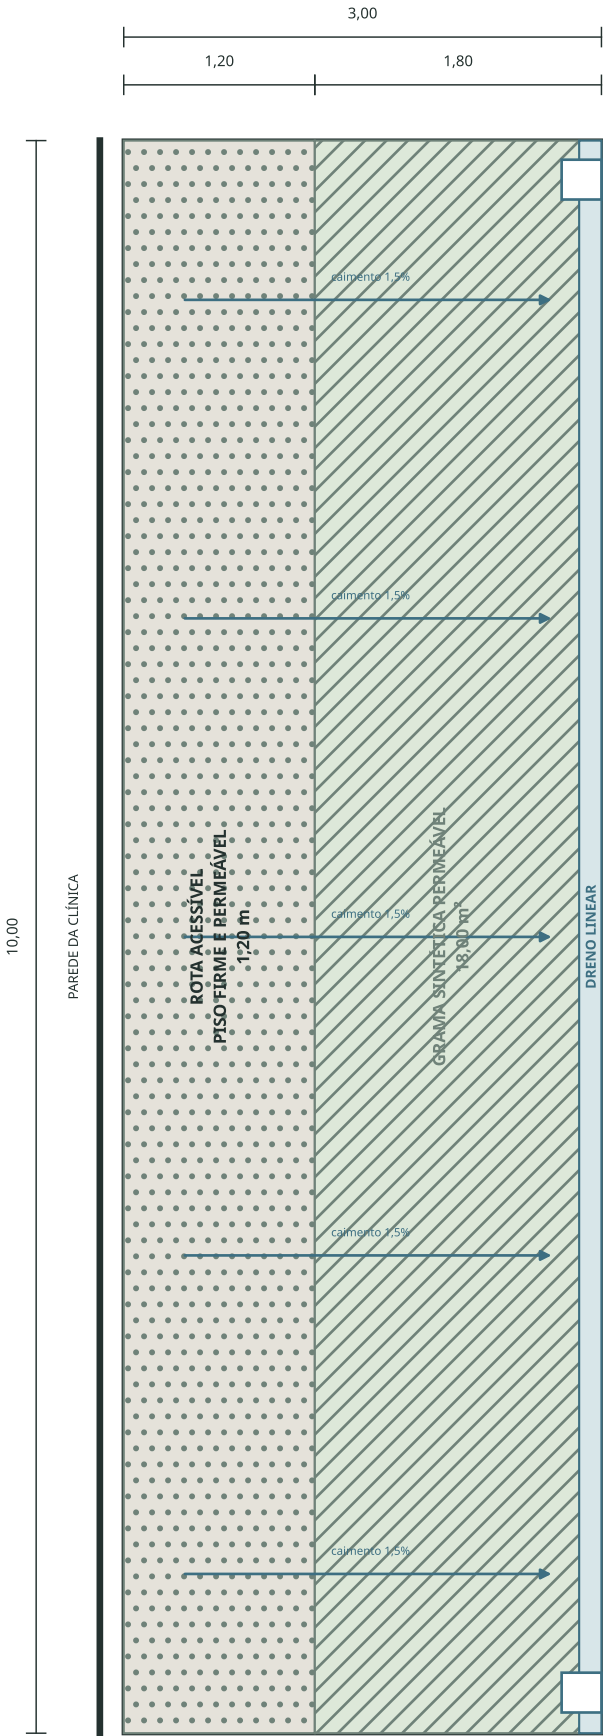

Não lançar água de cobertura na grama sem cálculo.  
Testar infiltração do solo e confirmar destino legal da água.

# LUMINA

SKIN INTELLIGENCE

## D-01

## ÁREA EXTERNA DRENANTE

Módulo-base 3,00 × 10,00 m ao lado da clínica — ajustar ao levantamento

### DADOS DO ANTEPROJETO

|                |                   |
|----------------|-------------------|
| Envoltória     | 6,00 × 10,00 m    |
| Área bruta     | 60,00 m²          |
| Pavimento      | Térreo            |
| Escala gráfica | Indicativa        |
| Implantação    | Maior de 2027     |
| Status         | Estudo preliminar |


### PREMISSAS DE PROJETO

- Módulo externo total: 30 m².
- Rota acessível: 12 m².
- Grama sintética: 18 m² + 8% de perdas.
- Caimento transversal indicativo: 1,5%.
- Base granular: 12-14 cm totais.
- Dreno linear: 10 m + duas caixas.
- Subleito, chuva de projeto e destino da água: a dimensionar localmente.

### Clínica Lumina Skin Intelligence

Anteprojeto-base ajustável

Conferir no local • Aprovação e RRT/ART obrigatórias

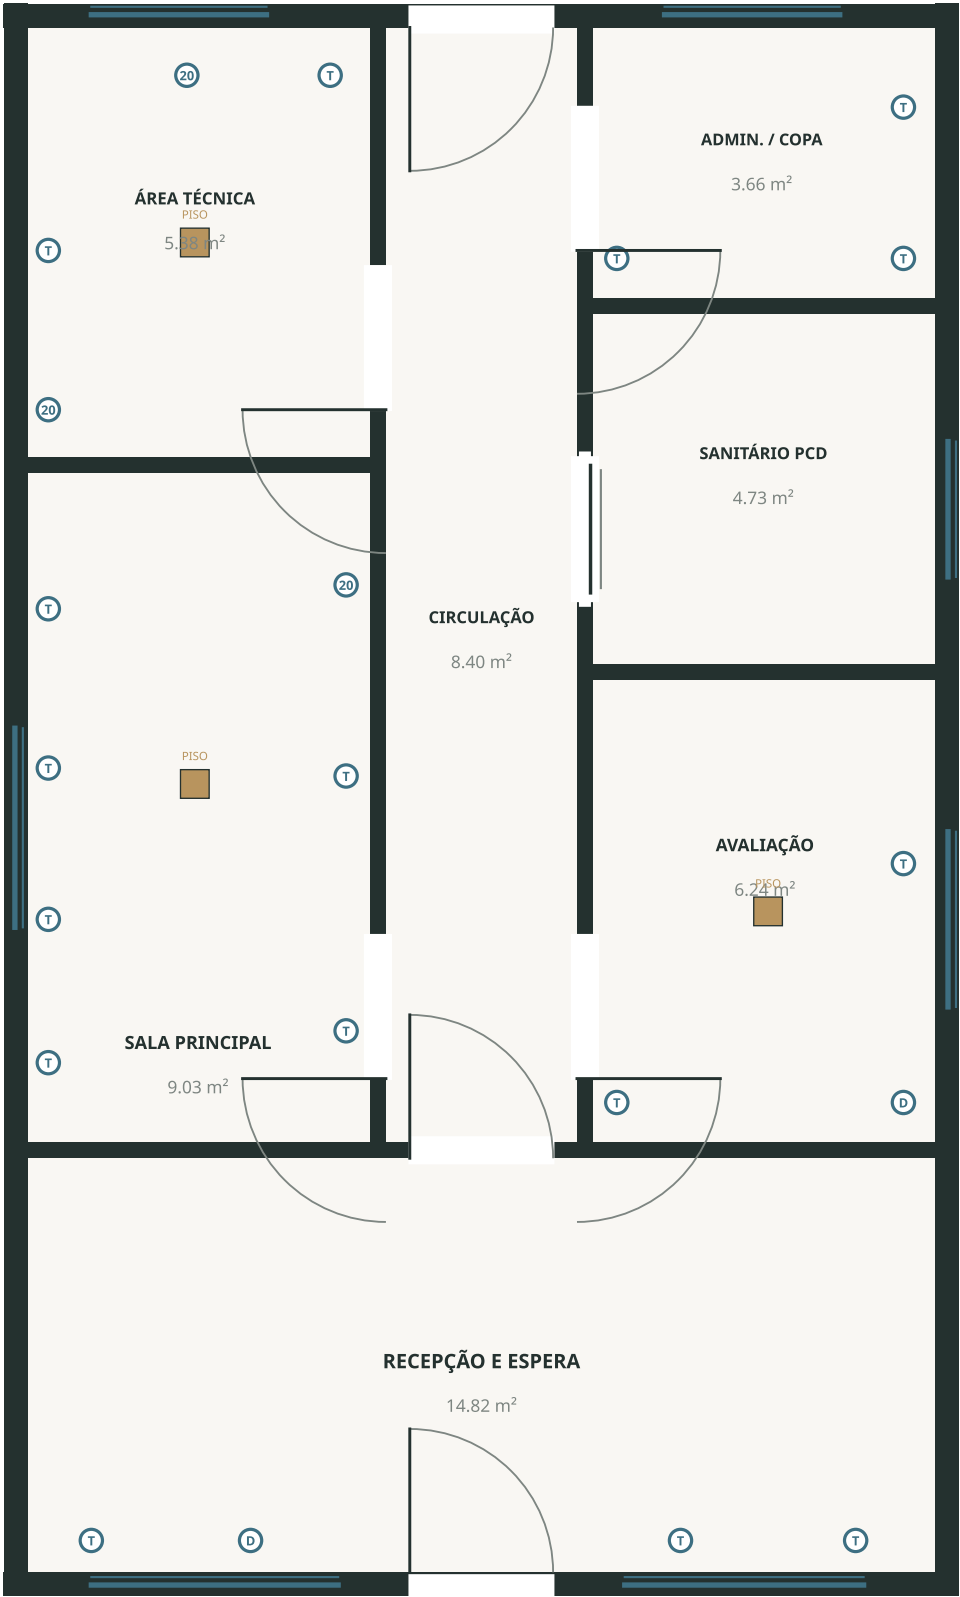

# LUMINA

SKIN INTELLIGENCE

E-01

## ELÉTRICA E DADOS

Pontos conceituais; circuitos e cargas a confirmar pelos fabricantes

### DADOS DO ANTEPROJETO

|                |                   |
|----------------|-------------------|
| Envoltória     | 6,00 × 10,00 m    |
| Área bruta     | 60,00 m²          |
| Pavimento      | Térreo            |
| Escala gráfica | Indicativa        |
| Implantação    | Maio de 2027      |
| Status         | Estudo preliminar |

### LEGENDA

- T tomada de uso geral
- 20 tomada dedicada 20 A\*
- D dados / rede
- caixa de piso\*

\*Confirmar tensão, potência, plugue, aterramento, DPS, DR e circuito exclu

### Clínica Lumina Skin Intelligence

Anteprojeto-base ajustável

Conferir no local • Aprovação e RRT/ART obrigatórias



# LUMINA

SKIN INTELLIGENCE

## E-02

## PONTOS DE EQUIPAMENTOS

Reservas conceituais; tensão, potência e plugues pelos manuais vigentes

### DADOS DO ANTEPROJETO

|                |                   |
|----------------|-------------------|
| Envoltória     | 6,00 × 10,00 m    |
| Área bruta     | 60,00 m²          |
| Pavimento      | Térreo            |
| Escala gráfica | Indicativa        |
| Implantação    | Maio de 2027      |
| Status         | Estudo preliminar |

### MAPA DE RESERVAS

#### EQ-01 HIFU

C01 dedicado 20 A\* • D opcional • sem dreno • carga: manual

#### EQ-02 Maca elétrica

C02 TUG 10 A\* • sem dados • sem dreno • carga: manual

#### EQ-03 LED/Laser

C03 reservado 20 A\* • sem dados • sem dreno • carga: manual

#### EQ-04 Autoclave/seladora

C04 dedicado 20 A\* • sem dados • ES condicional • carga: manual

#### EQ-05 Câmara conservação

\*Reserva indicativa; confirmar tensão, potência, plugue, DR, DPS, aterramento e fabricante antes da instalação


#### EQ-06 Fotografia

C06 TUG 10 A\* • D obrigatório • sem dreno • carga: manual

Conferir no local • Aprovação e RRT/ART obrigatórias

#### EQ-07 TI/impressora

C07 TUG 10 A\* • D obrigatório • sem dreno • carga: manual

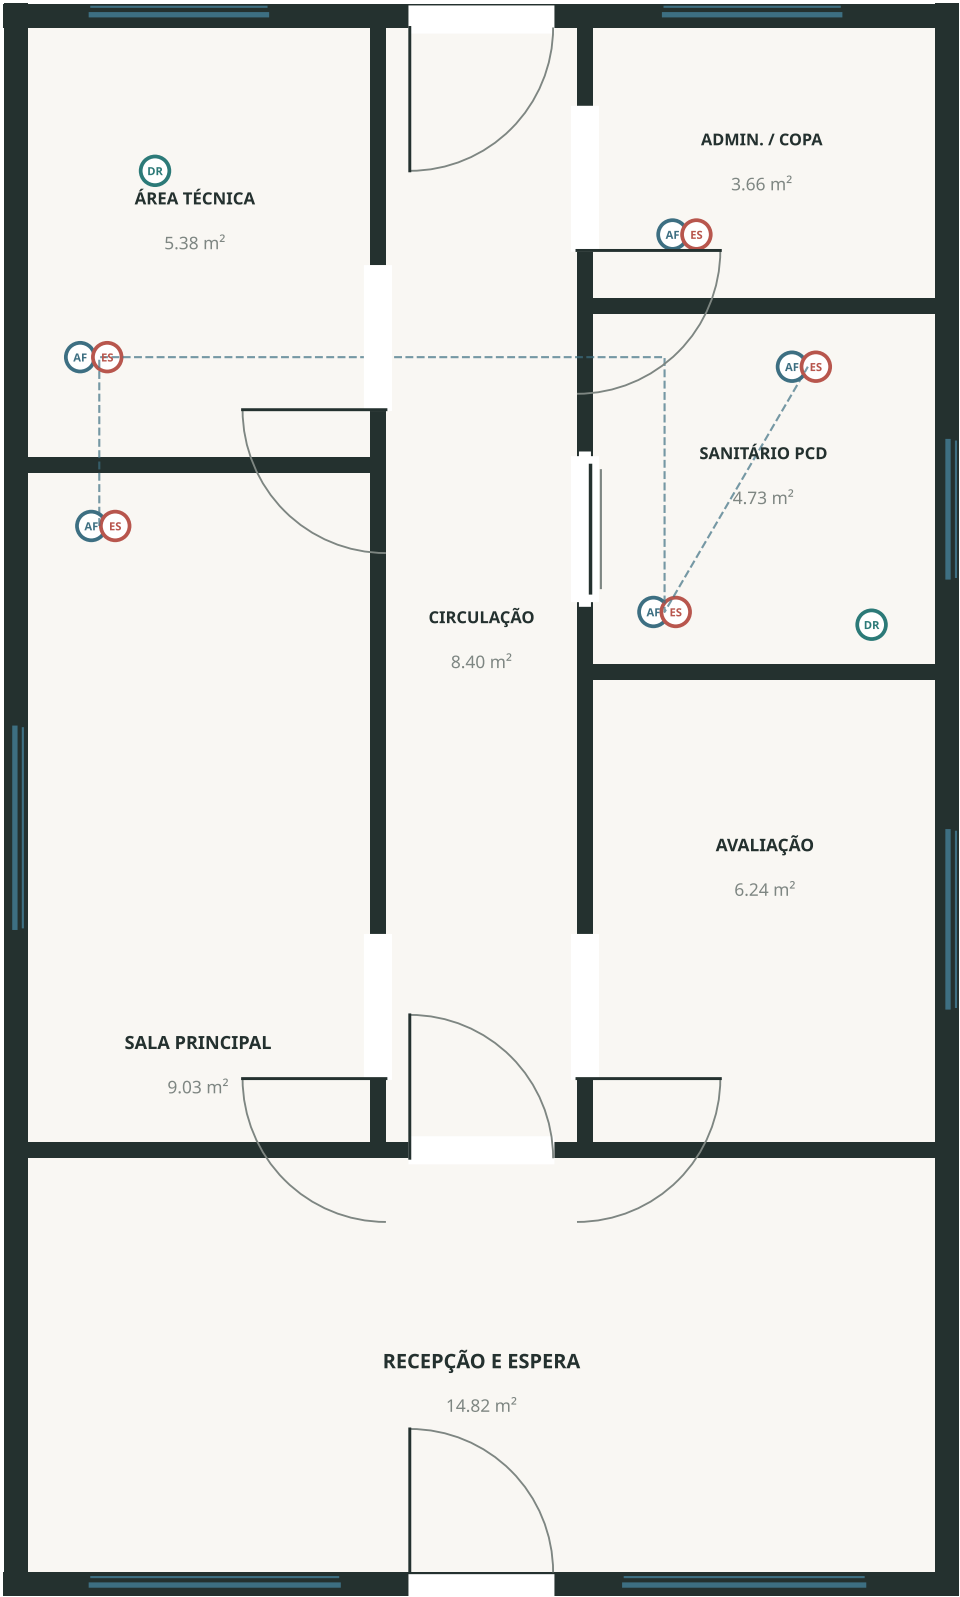

# LUMINA

SKIN INTELLIGENCE

H-01

## HIDRÁULICA E SANITÁRIA

Água fria, esgoto, ralos e parede hidráulica concentrada

### DADOS DO ANTEPROJETO

|                |                   |
|----------------|-------------------|
| Envoltória     | 6,00 × 10,00 m    |
| Área bruta     | 60,00 m²          |
| Pavimento      | Térreo            |
| Escala gráfica | Indicativa        |
| Implantação    | Maio de 2027      |
| Status         | Estudo preliminar |

### LEGENDA


AF água fria  
ES esgoto  
DR dreno / ralo

Concentrar prumadas e validar diâmetros, ventilação sanitária, caixas, decl

### Clínica Lumina Skin Intelligence

Anteprojeto-base ajustável

Conferir no local • Aprovação e RRT/ART obrigatórias

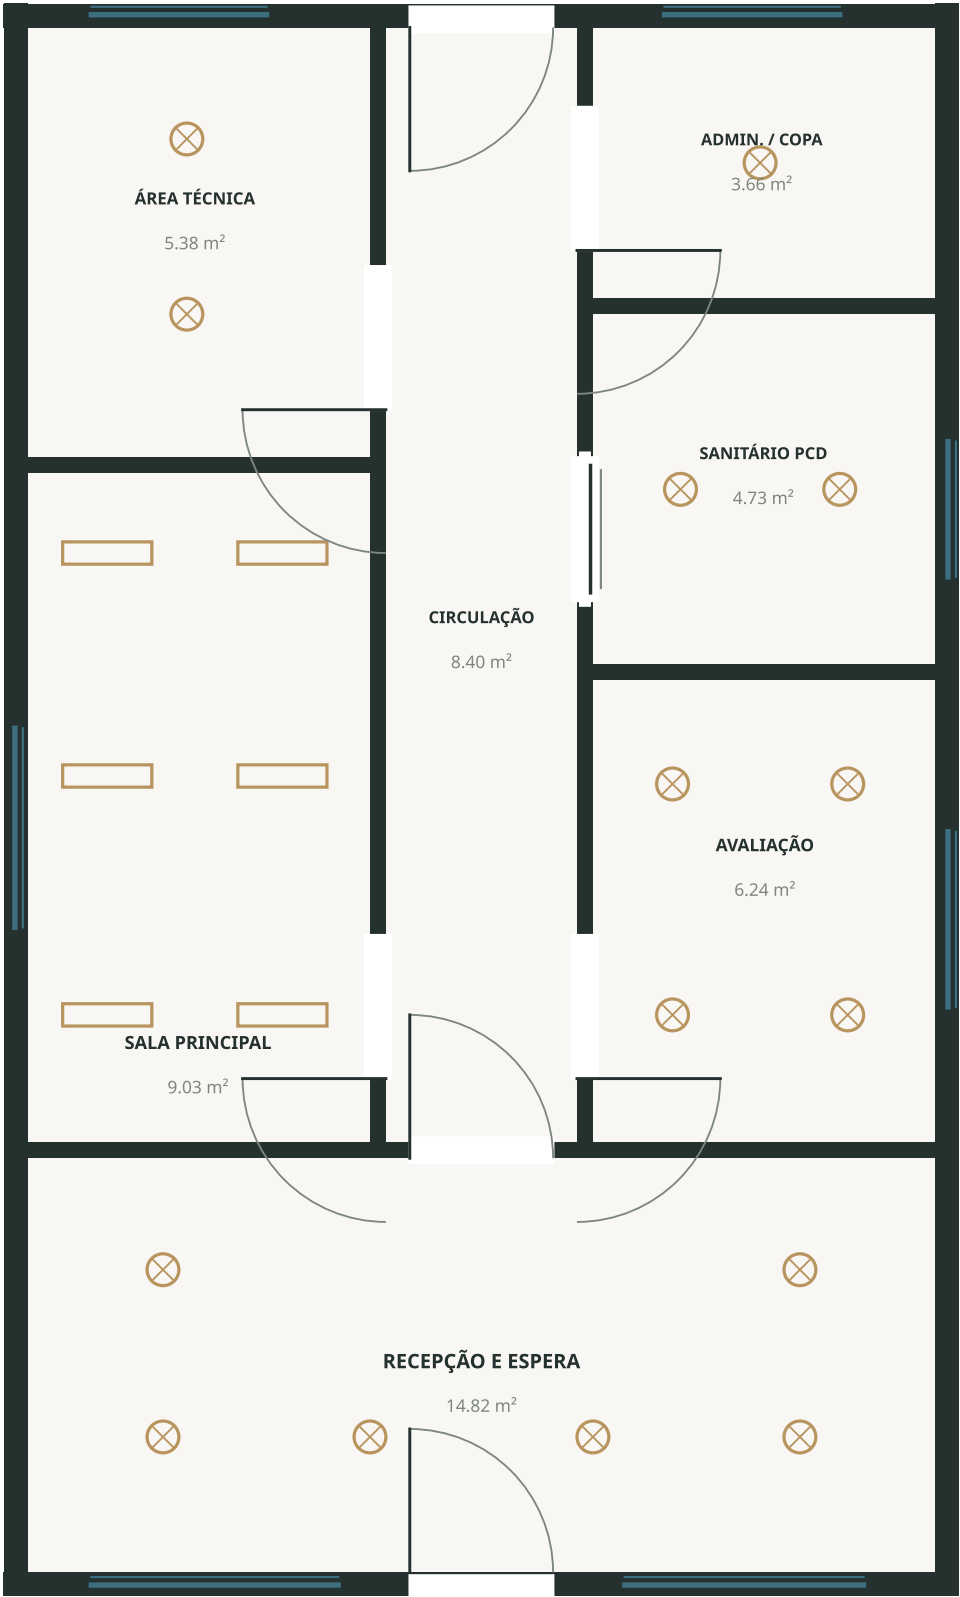

# LUMINA

SKIN INTELLIGENCE

L-01

## FORRO E ILUMINAÇÃO

Iluminação geral, clínica e de acolhimento — níveis a calcular

### DADOS DO ANTEPROJETO

|                |                   |
|----------------|-------------------|
| Envoltória     | 6,00 × 10,00 m    |
| Área bruta     | 60,00 m²          |
| Pavimento      | Térreo            |
| Escala gráfica | Indicativa        |
| Implantação    | Maio de 2027      |
| Status         | Estudo preliminar |


### DIRETRIZES

- Luz acolhedora na espera.
- Luz neutra e uniforme nas salas.
- Alto índice de reprodução de cor na avaliação/fotografia.
- Comandos independentes por cena.
- Evitar ofuscamento sobre a maca.
- Projeto luminotécnico deve confirmar iluminância e potência.

### Clínica Lumina Skin Intelligence

Anteprojeto-base ajustável

Conferir no local • Aprovação e RRT/ART obrigatórias

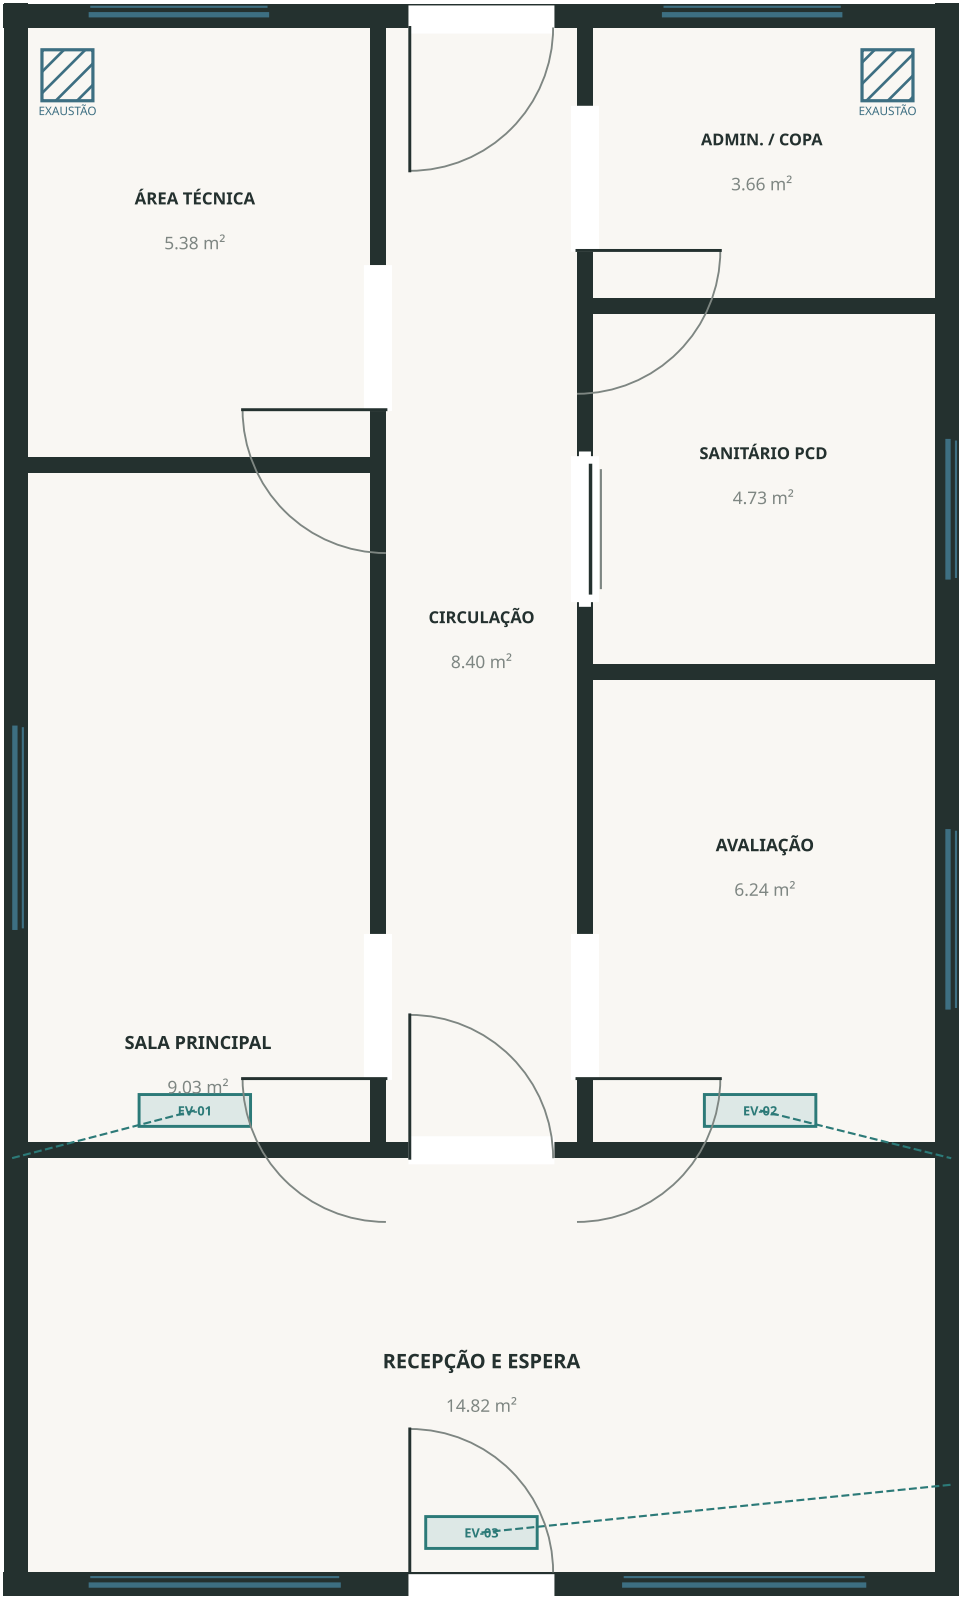

# LUMINA

SKIN INTELLIGENCE

M-01

## CLIMATIZAÇÃO E VENTILAÇÃO

Evaporadoras, condensação, renovação e exaustão conceituais

### DADOS DO ANTEPROJETO

|                |                   |
|----------------|-------------------|
| Envoltória     | 6,00 × 10,00 m    |
| Área bruta     | 60,00 m²          |
| Pavimento      | Térreo            |
| Escala gráfica | Indicativa        |
| Implantação    | Maio de 2027      |
| Status         | Estudo preliminar |

### DIRETRIZES


- Dimensionar carga térmica por ambiente.
- Não direcionar jato sobre paciente.
- Prever drenos sifonados e acesso para manutenção.
- Confirmar renovação de ar e exaustão conforme uso e exigência local.
- Não instalar condensadoras em área sem ventilação.

### Clínica Lumina Skin Intelligence

Anteprojeto-base ajustável

Conferir no local • Aprovação e RRT/ART obrigatórias



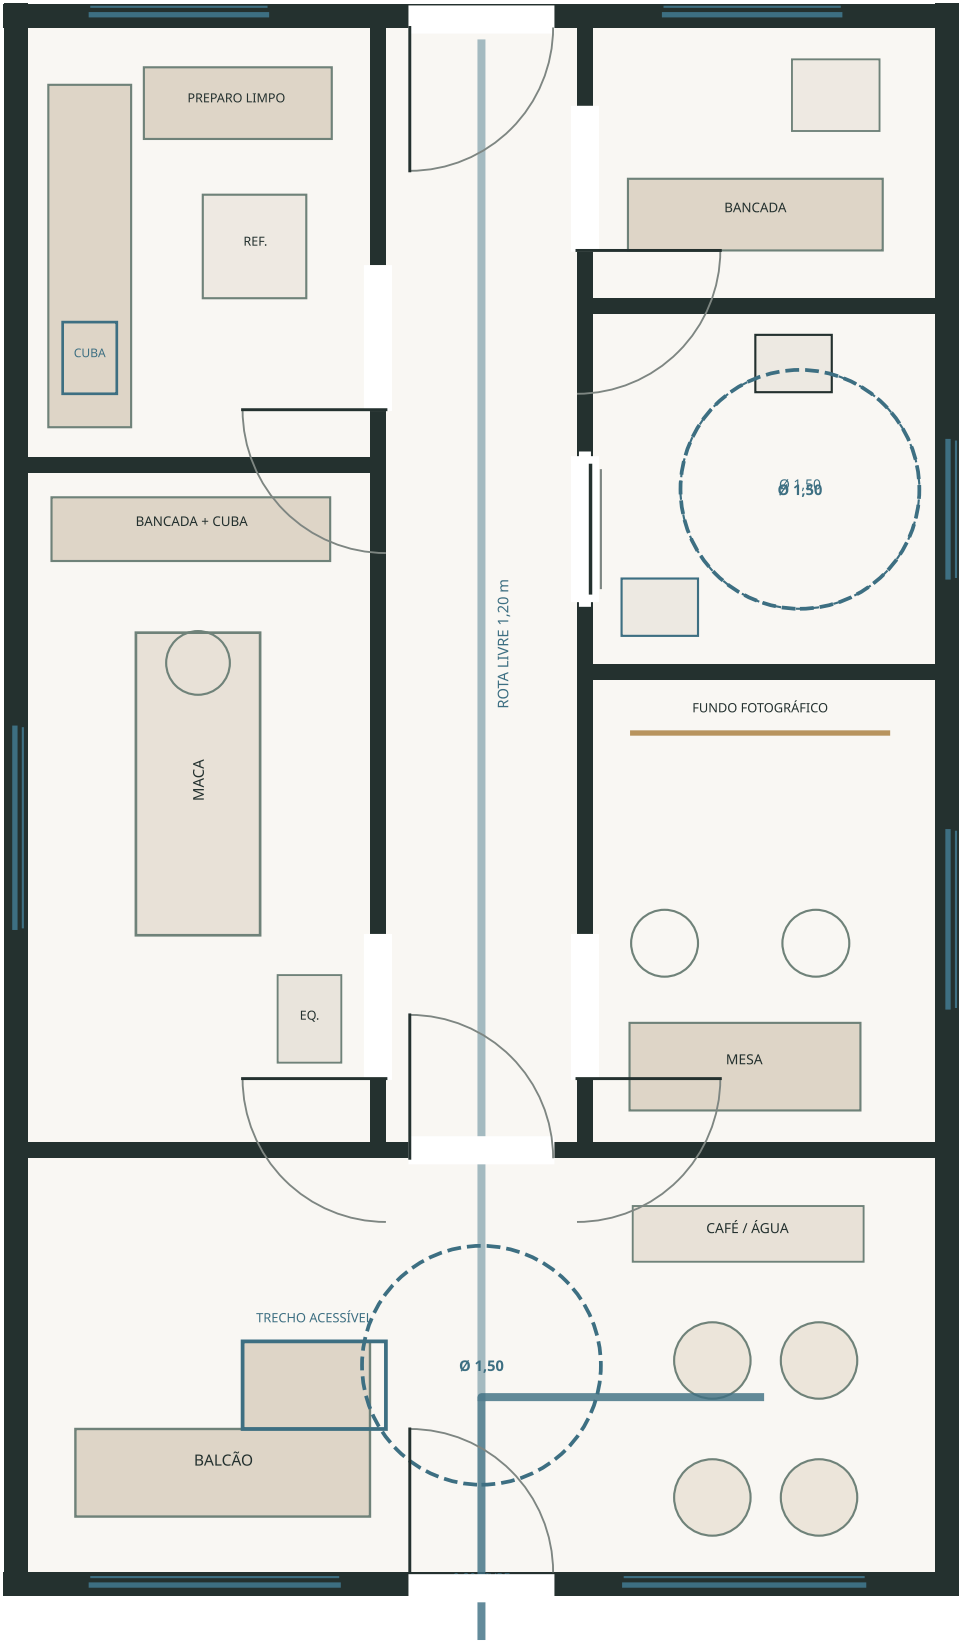

# LUMINA

SKIN INTELLIGENCE

A-03

## ACESSIBILIDADE

Rota acessível, giros, vãos e balcão conforme NBR 9050:2020

### DADOS DO ANTEPROJETO

|                |                   |
|----------------|-------------------|
| Envoltória     | 6,00 × 10,00 m    |
| Área bruta     | 60,00 m²          |
| Pavimento      | Térreo            |
| Escala gráfica | Indicativa        |
| Implantação    | Maio de 2027      |
| Status         | Estudo preliminar |


### PARÂMETROS

- Portas: vão livre ≥ 0,80 m.
- Corredor central: 1,20 m.
- Giro: Ø 1,50 m.
- Sanitário com transferências e porta de correr.
- Balcão: trecho ≥ 0,90 m e altura 0,75–0,85 m.
- Piso interno: inclinação transversal ≤ 2%.

### Clínica Lumina Skin Intelligence

Anteprojeto-base ajustável

Conferir no local • Aprovação e RRT/ART obrigatórias

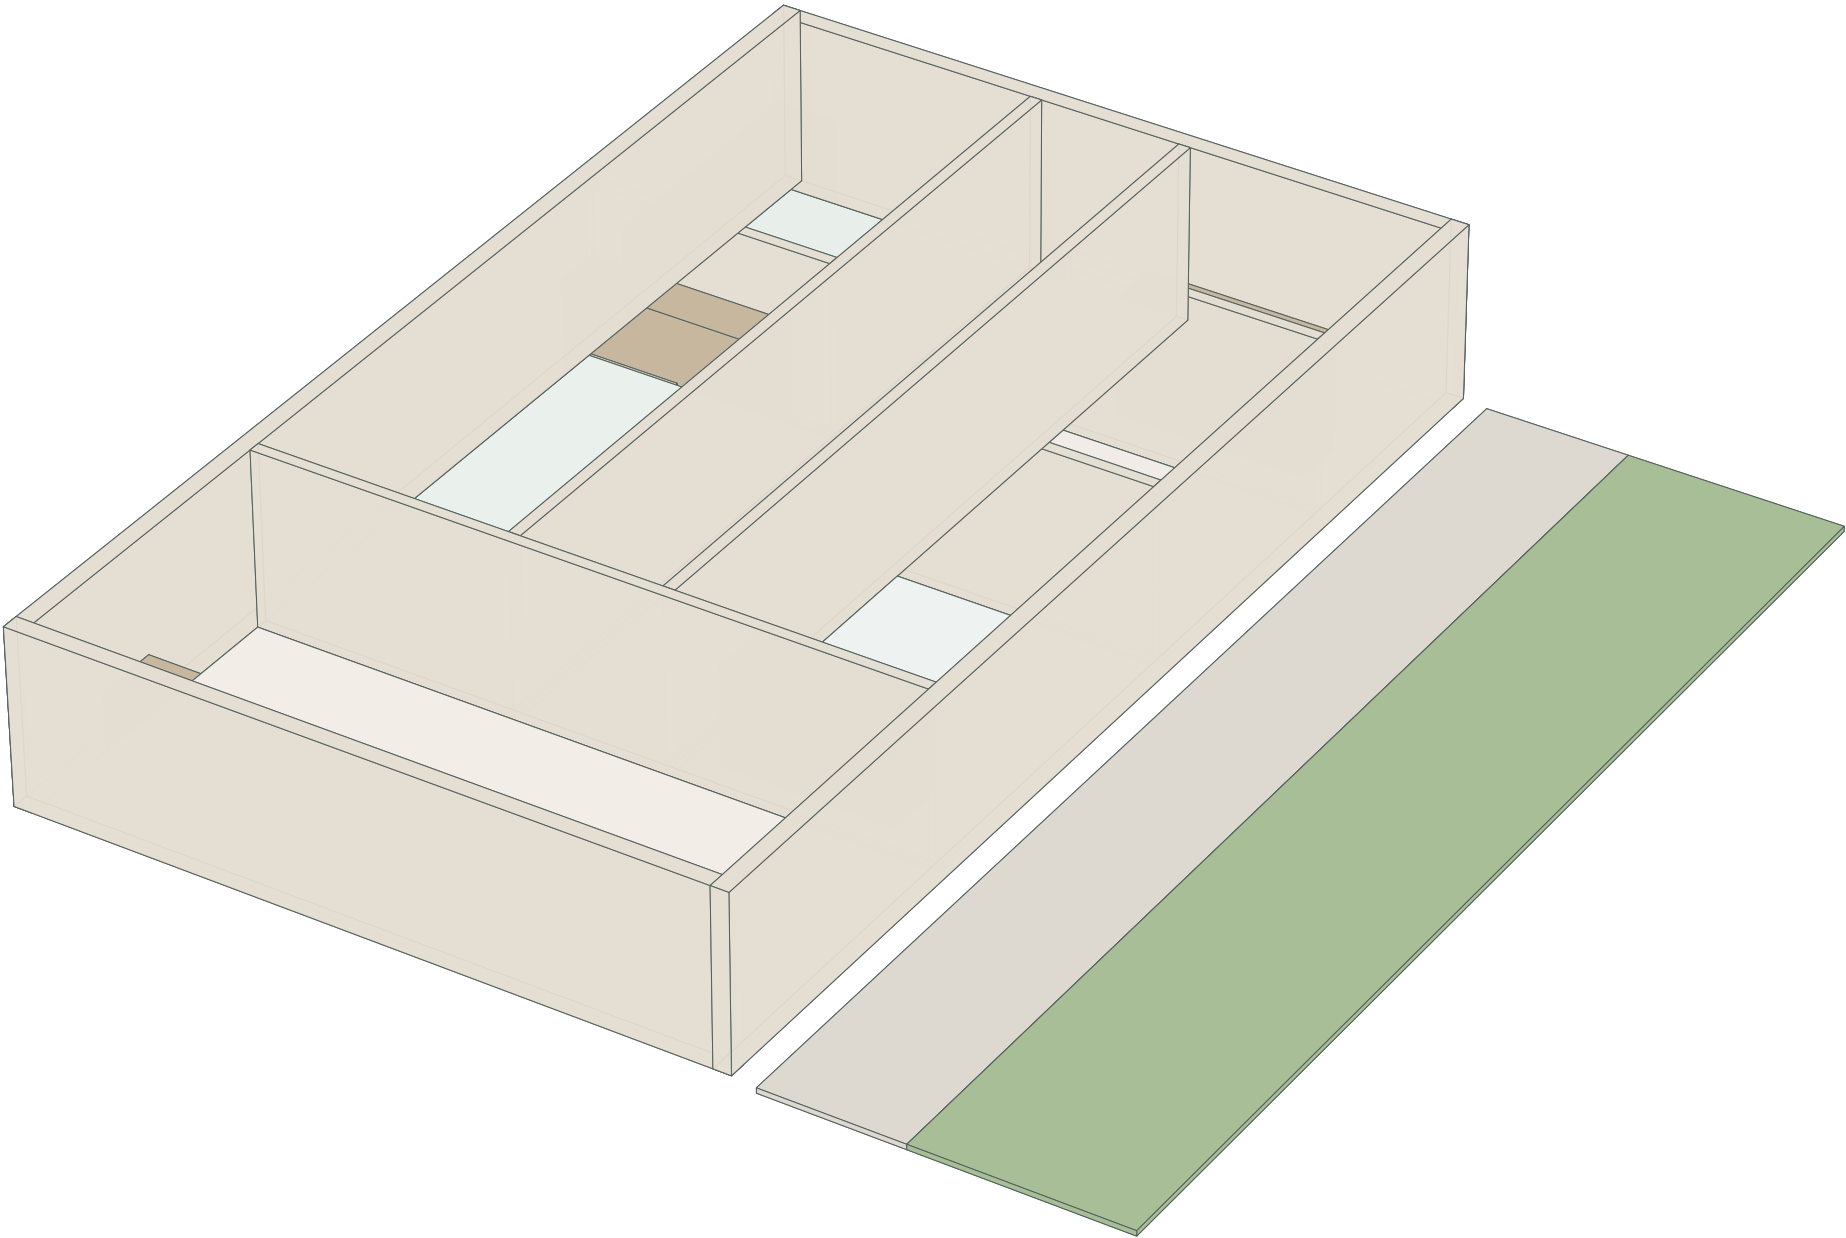

# LUMINA

SKIN INTELLIGENCE

MQ-01

## MAQUETE 3D

Axonométrica interna + área externa drenante; modelo conceitual sem cobertura

### DADOS DO ANTEPROJETO

|                |                   |
|----------------|-------------------|
| Envoltória     | 6,00 × 10,00 m    |
| Área bruta     | 60,00 m²          |
| Pavimento      | Térreo            |
| Escala gráfica | Indicativa        |
| Implantação    | Maio de 2027      |
| Status         | Estudo preliminar |

### LEITURA DO MODELO

Maquete sem cobertura para leitura dos ambientes, circulação e mobiliário. Não representa estrutura, fundações, texturas finais ou instalações ocultas. Usar com as pranchas A-01 a E-02 e atualizar após levantamento do terreno.

### Clínica Lumina Skin Intelligence

Anteprojeto-base ajustável

Conferir no local • Aprovação e RRT/ART obrigatórias